


Upper floor

- From the centre outwards:
- Net Ø 7.80 usable (opening Ø 8.50)
 - Padded edge 0.35 m on the ring beam
 - Ring walkway 1.10 m (up to 1.38 m at the posts)
 - 9 rooms, each ≈ 17 m², 3.4 m wide at the door, 5.9 m at the outer wall, 4.1 m deep
 - Spiral stair in the 10th slot, on up to the roof
- Clear height in rooms 2.60 m

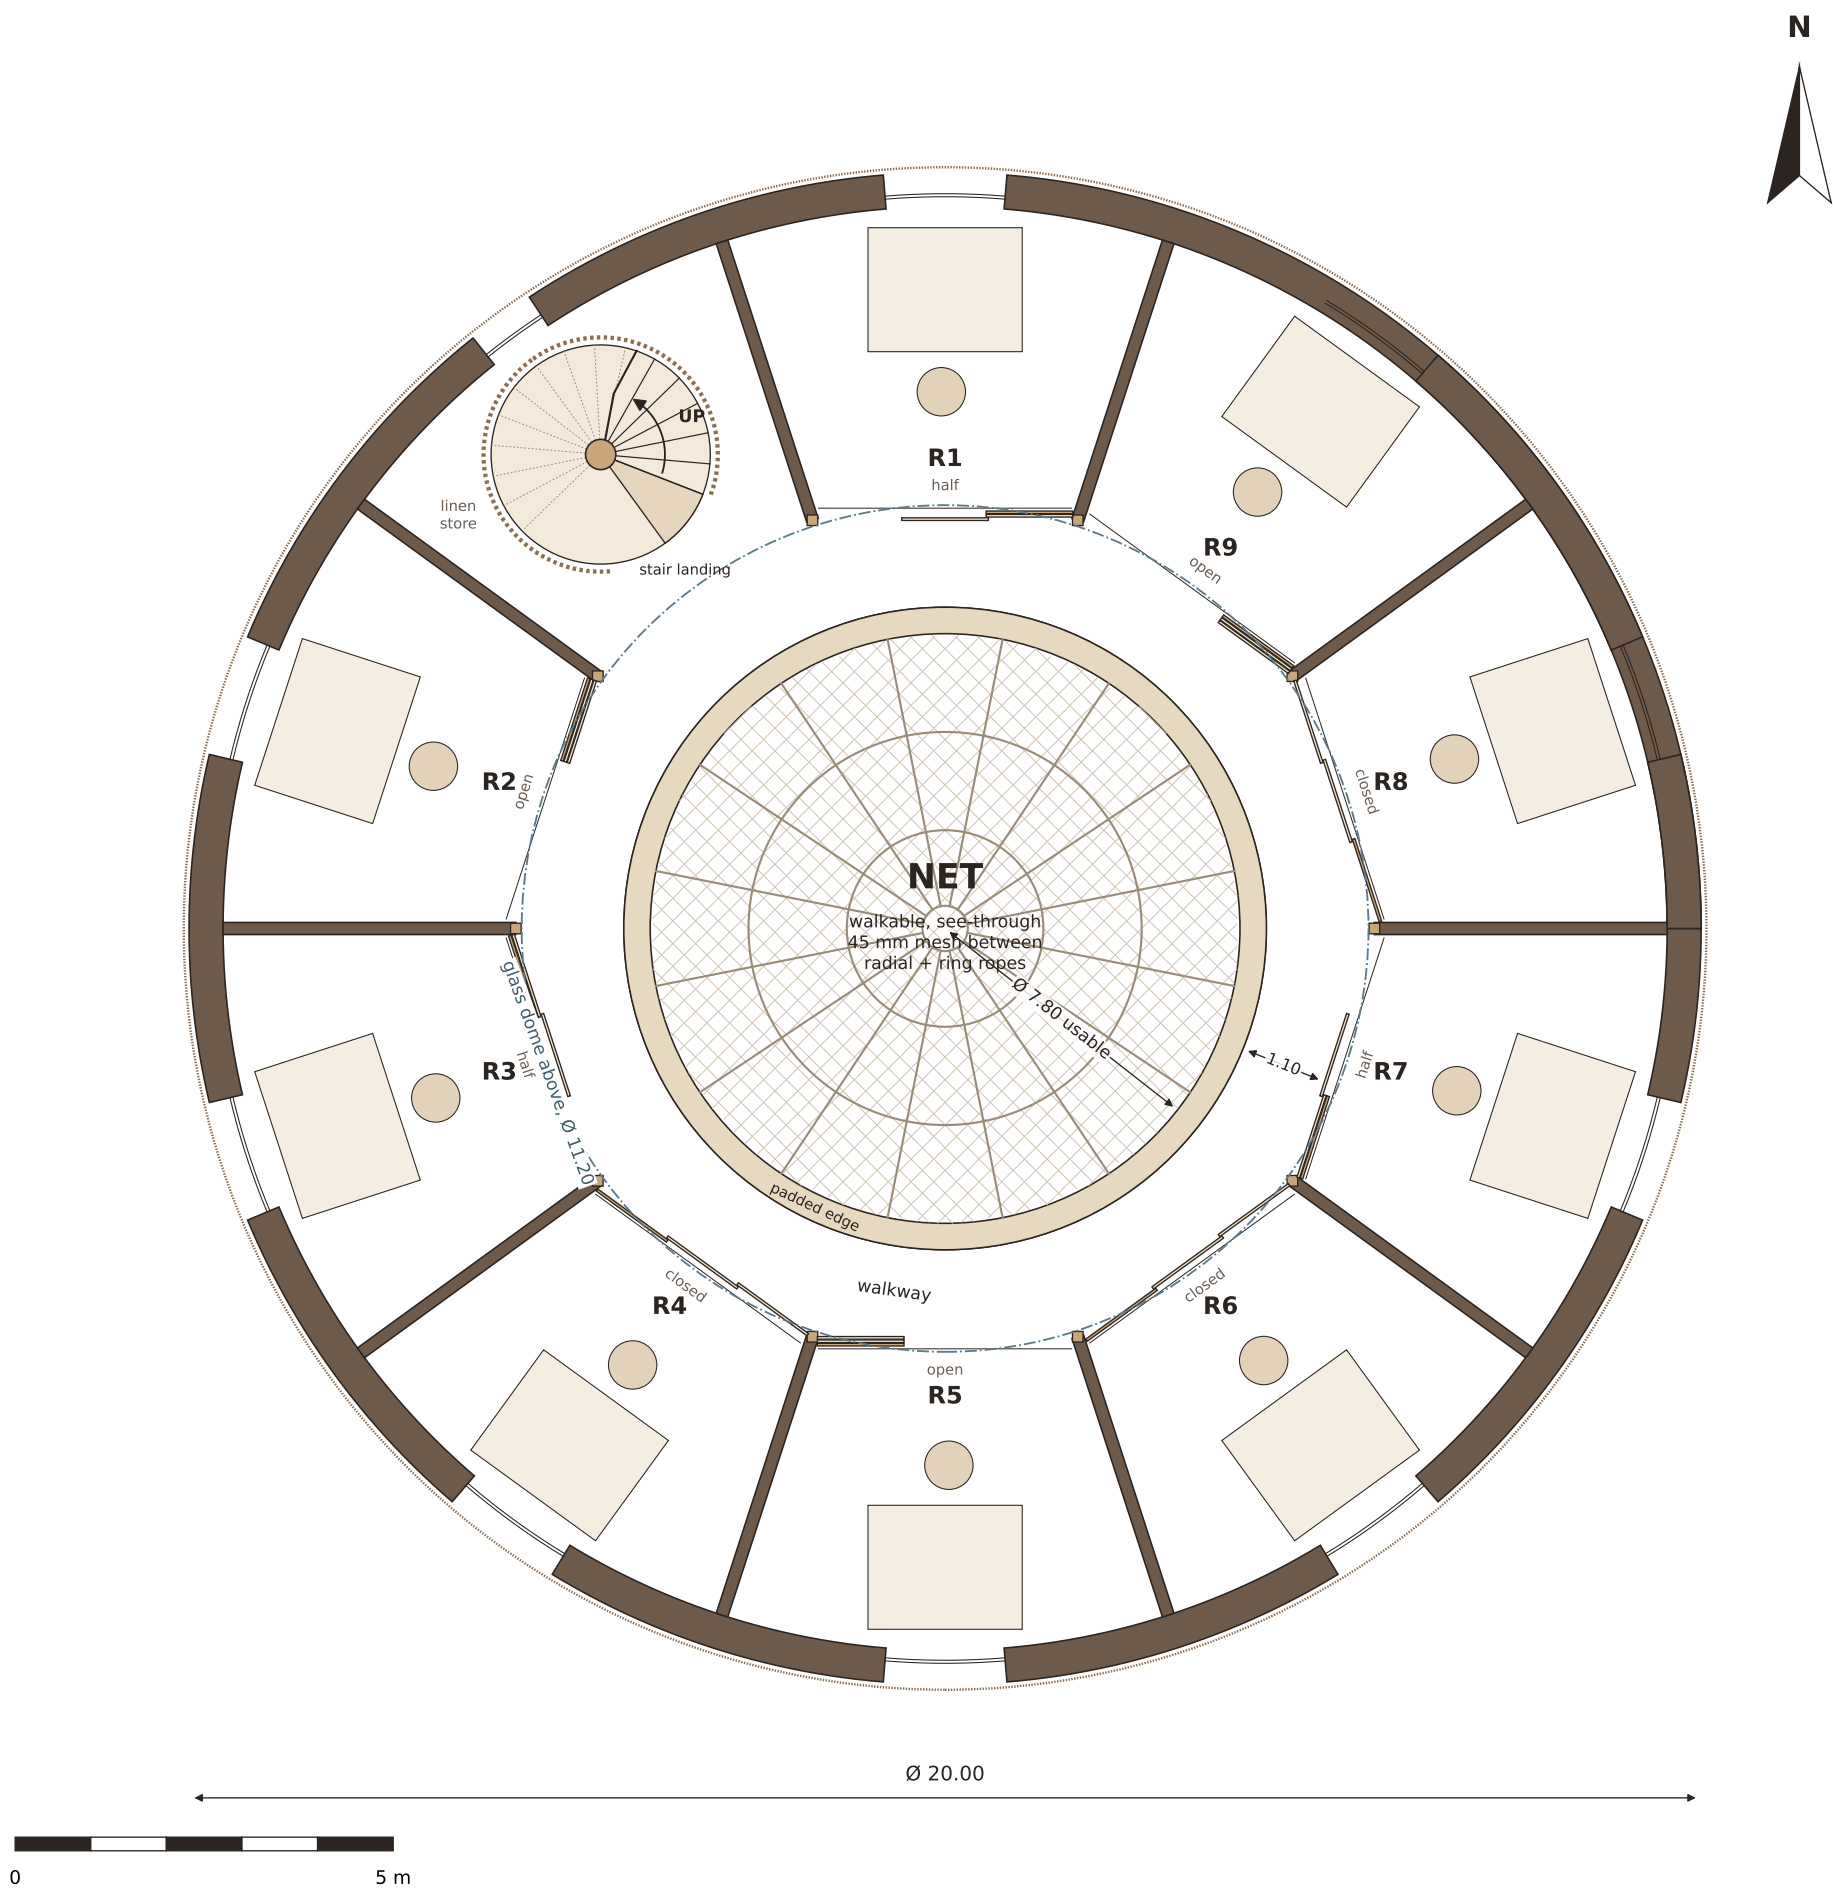

- Rooms
- Front: 3 shoji-type panels (oak frame, linen or paper-laminate infill). One fixed, two sliding: closed / half (1.1 m) / open (2.2 m)
 - One low window per room (sill 0.45 m, 1.6 m wide) behind outside larch battens: light and air, no view in; inside shutter or curtain
 - Acoustic partitions 160 mm, clay plaster
 - Floor mattress, cushions, lanterns, shelf niche

- Stair (hall -> upper floor -> roof terrace)
- Helical stair around a wooden trunk, Ø 2.9 m, treads 1.25 m wide, in a slatted larch screen
 - Exactly one turn per storey: 22 risers × 180 mm, so you get on and off at the front of the slot
 - Going 243 mm on the walking line (r = 0.85 m)
 - Upper floor -> terrace: 17 risers × 185 mm
 - A straight flight (≈5.3 m) does not fit the 4.1 m slot; a stacked U-stair leaves no room for the roof exit next to the dome.