


Upper floor

From the centre outwards:

- Net Ø 7.80 usable (opening Ø 8.50)
 - Padded edge 0.35 m on the ring beam
 - Ring walkway 1.10 m (up to 1.55 m at the posts)
 - 7 rooms, each ≈ 24 m²: 4.5 m wide at the door, 7.9 m at the straight outer wall, 4.1 m deep
 - Stair segment: spiral stair, WC + shower, door to the external stair
- Clear height in rooms 2.60 m

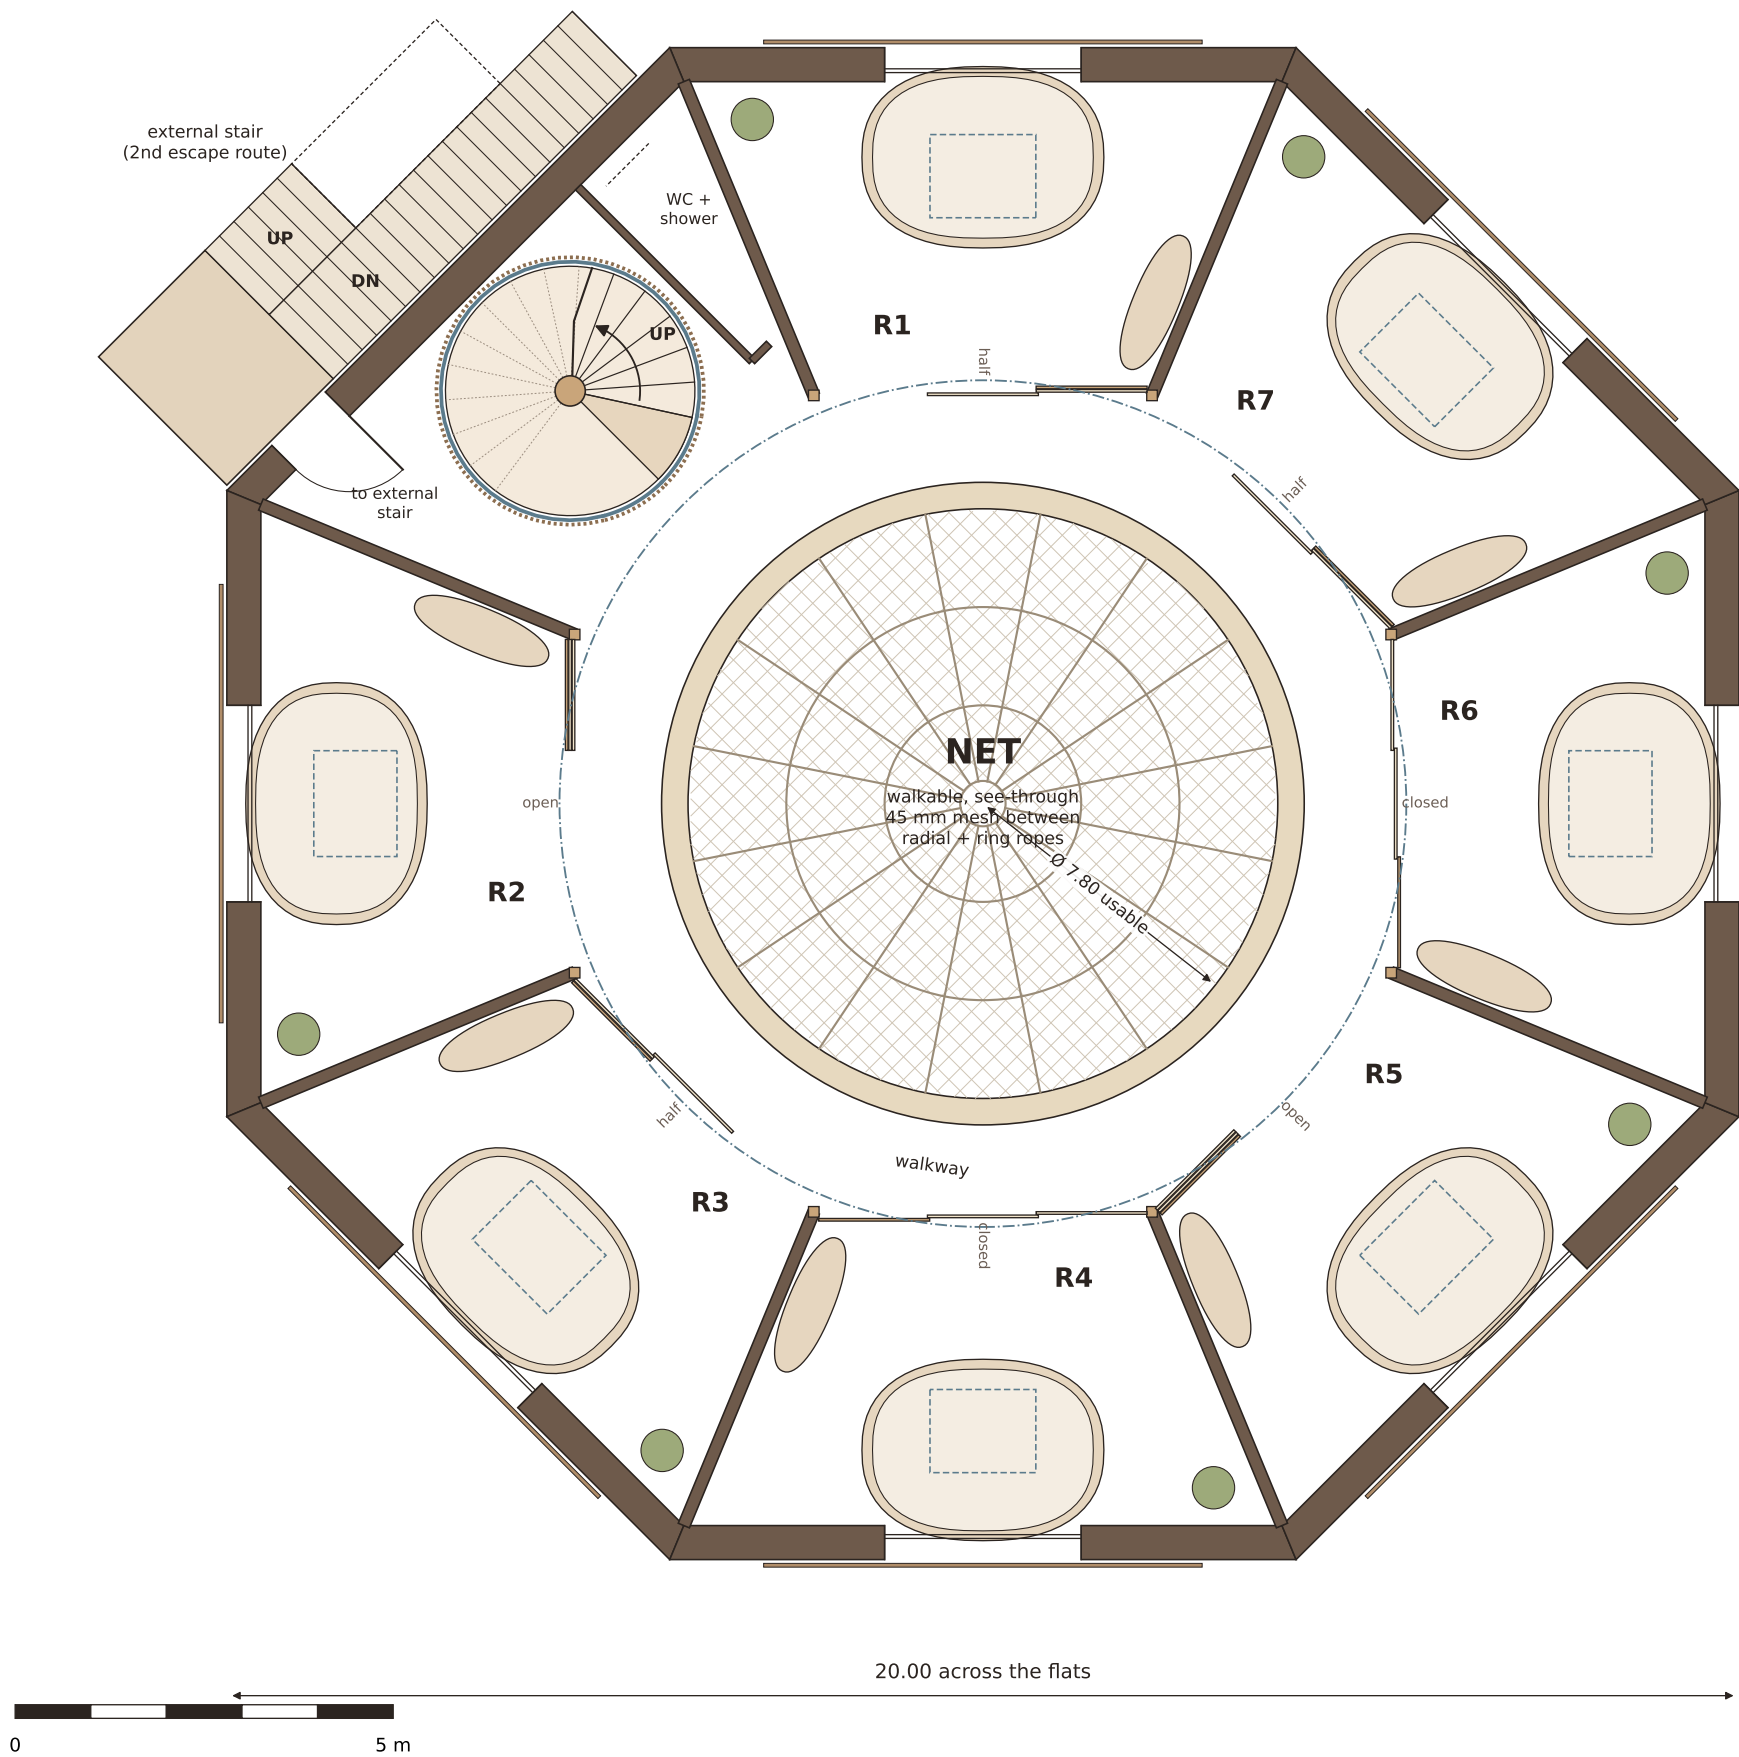

Rooms (7 × ≈ 24 m², for 1-3 people, also overnight)

- Front: 3 shoji-type panels (oak frame, linen / paper infill): closed / half (1.4 m) / open (2.9 m); a small signal lantern by each door: lit = welcome / ask, dark = private
- Earthen sleeping nest under the window, clay bench, sheepskins, lanterns, plants – no hotel furniture
- Big window 2.60 × 1.65 m (sill 0.45 m, fixed safety glass up to 0.90 m), sliding larch shutters outside; the opening part is a rescue window (≥ 0.90 × 1.20 m)
- Skylight 1.40 × 1.10 m over the nest: walk-on frosted glass in the terrace (light, no view in)
- Acoustic partitions 160 mm, clay plaster

Stair (DIN 18065, as a necessary stair)

- Spiral stair around a timber trunk, Ø 3.3 m, tread width 1.45 m, one turn per storey
- 22 risers × 180 mm, going 264 mm on the walking line (r = 0.925 m) · to the terrace 17 × 185 mm
- Own enclosure: fire-rated glass drum, doors held open on magnets, exit straight outside, smoke vent on top
- External stair on the same face = 2nd escape route