


Roof terrace

- Flat roof over the rooms as a sun terrace around the dome, deck at +7.28
- South side (SW-S-SE): 6 daybeds, sun sails, 1.80 m slatted privacy screen
 - West / east: loungers; north / north-east: big floor mattresses in the shade, planters, grasses
 - Dome on a 45 cm upstand = bench ring
 - Frosted walk-on skylights over each room
 - Reached by the external stair only: going up to the terrace means going outside anyway

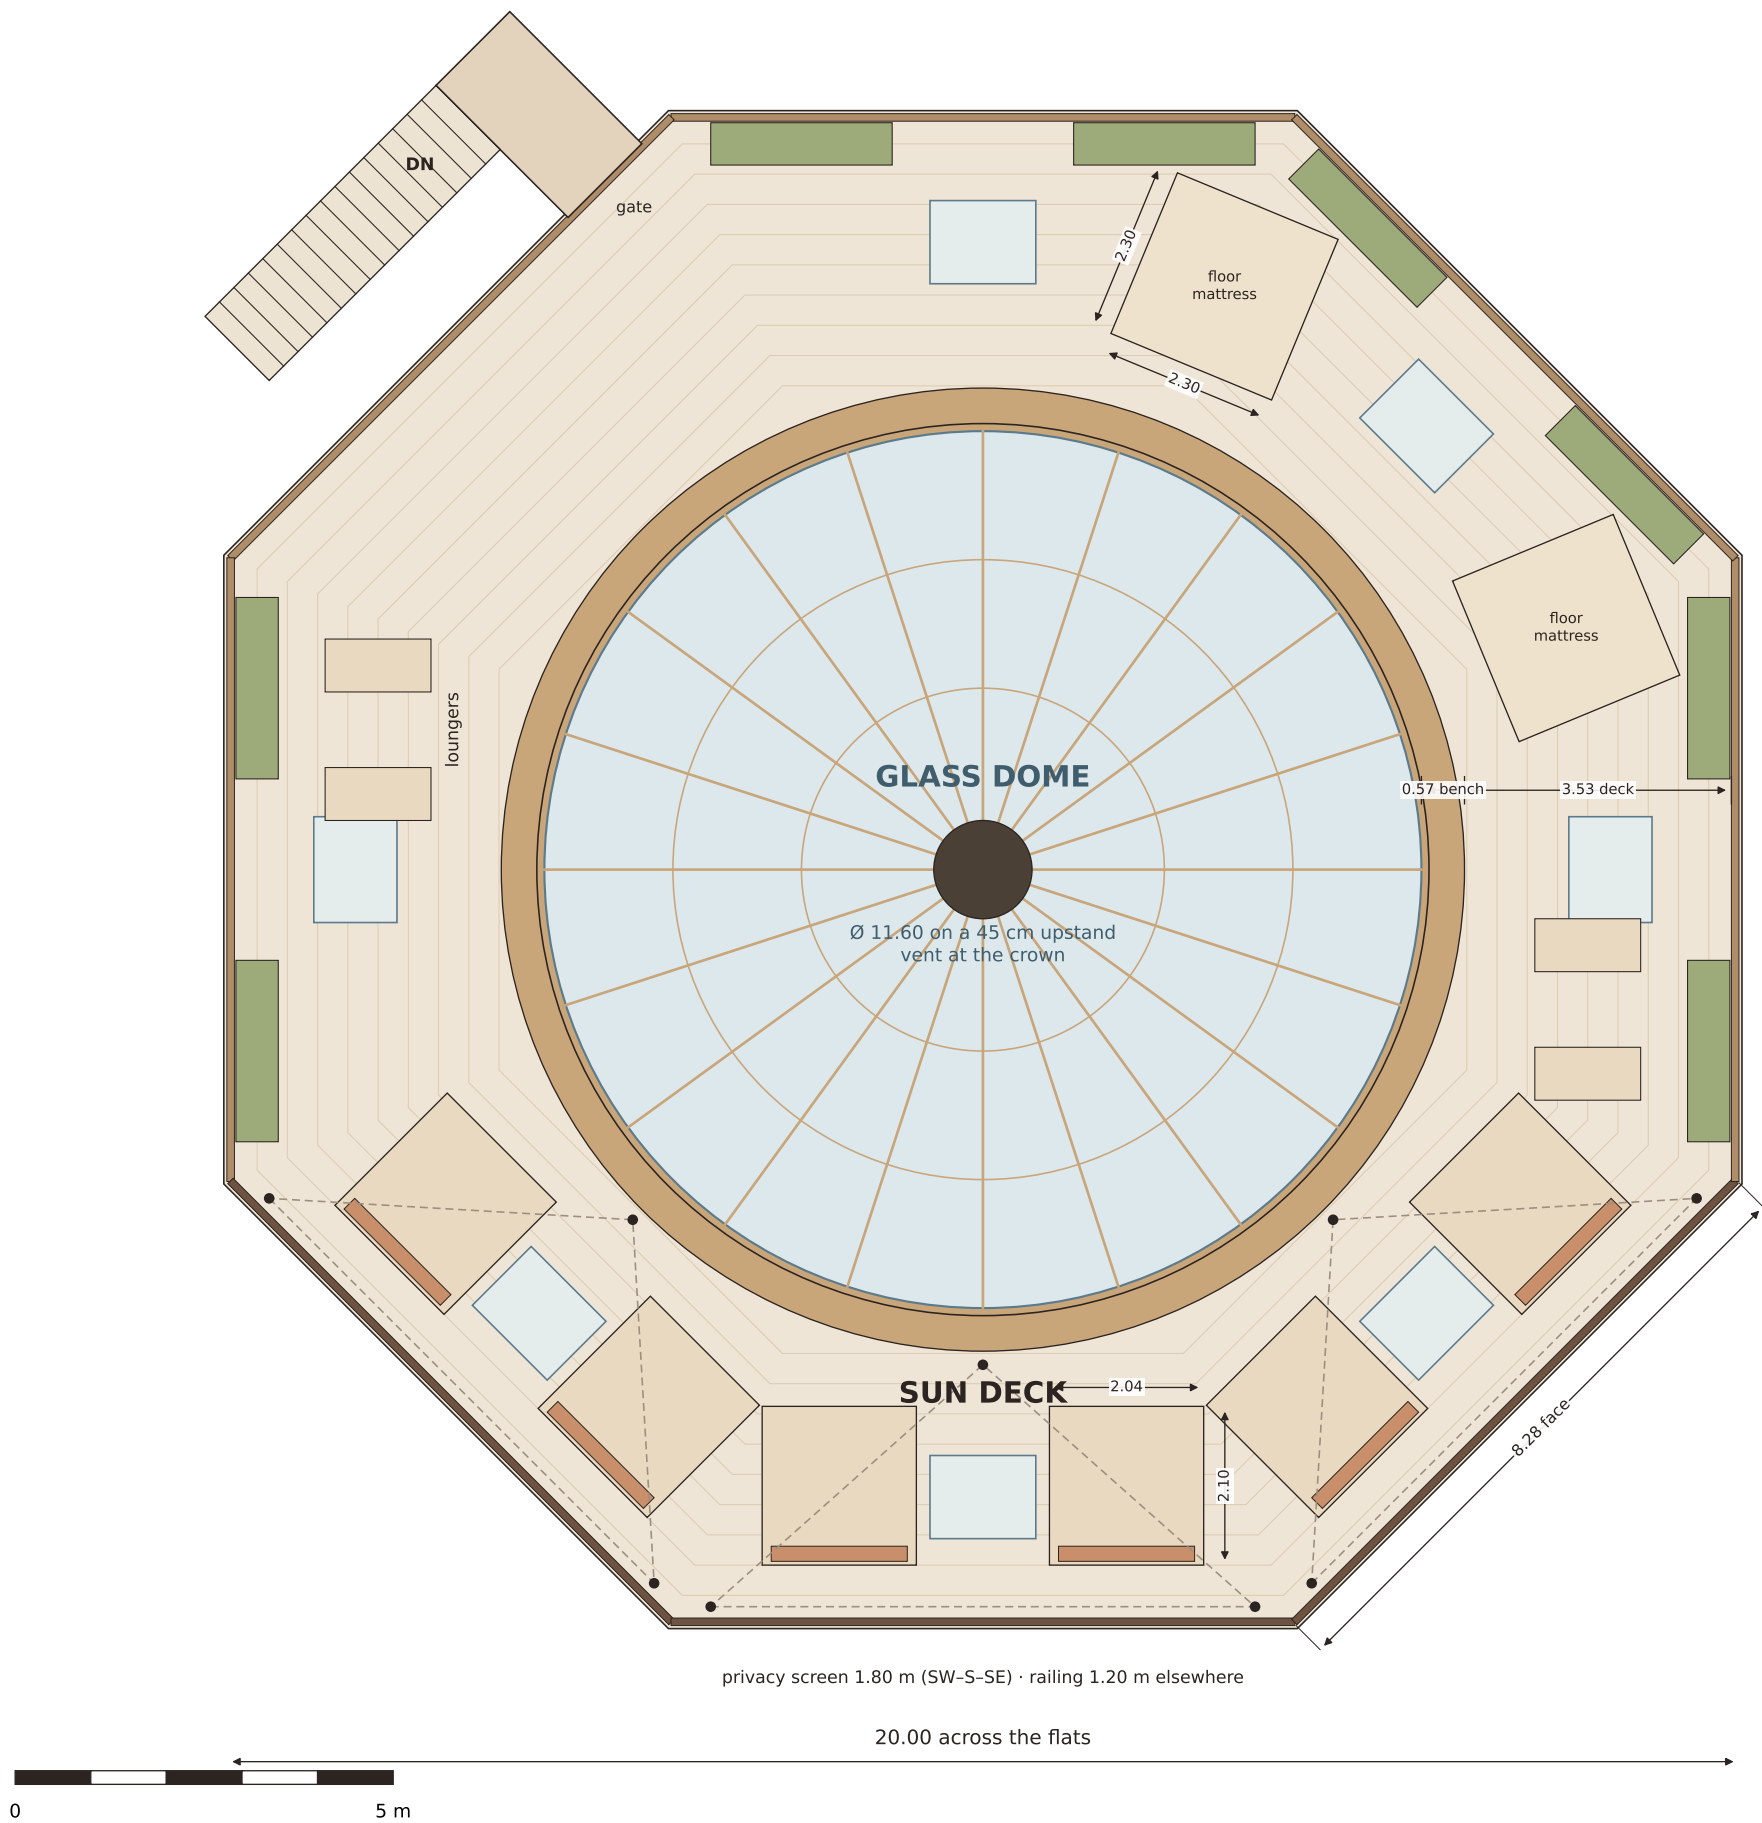

- Notes
- Walkable flat roof: imposed load $\approx 4 \text{ kN/m}^2$, falls to internal outlets, deck on pedestals
 - Skylights: walk-on laminated safety glass, frosted
 - Sun sails are demountable (winter, storms)
 - Annex keeps a green sedum roof (not walkable)