


Upper floor

- From the centre outwards:
- Net Ø 7.80 usable (opening Ø 8.60)
 - Padded edge 0.40 m on the ring beam
 - Ring walkway 1.25 m (up to 1.75 m at the posts)
 - 6 rooms, each ≈ 23 m²: 4.6 m wide at the door, 7.9 m at the straight outer wall, 3.8 m deep
 - Shared bathroom (north): 2 WCs, walk-in group shower, 2 basins – all gender
 - Stair segment: stair, linen / laundry, landing with the door to the external stair
- Clear height in rooms 2.60 m

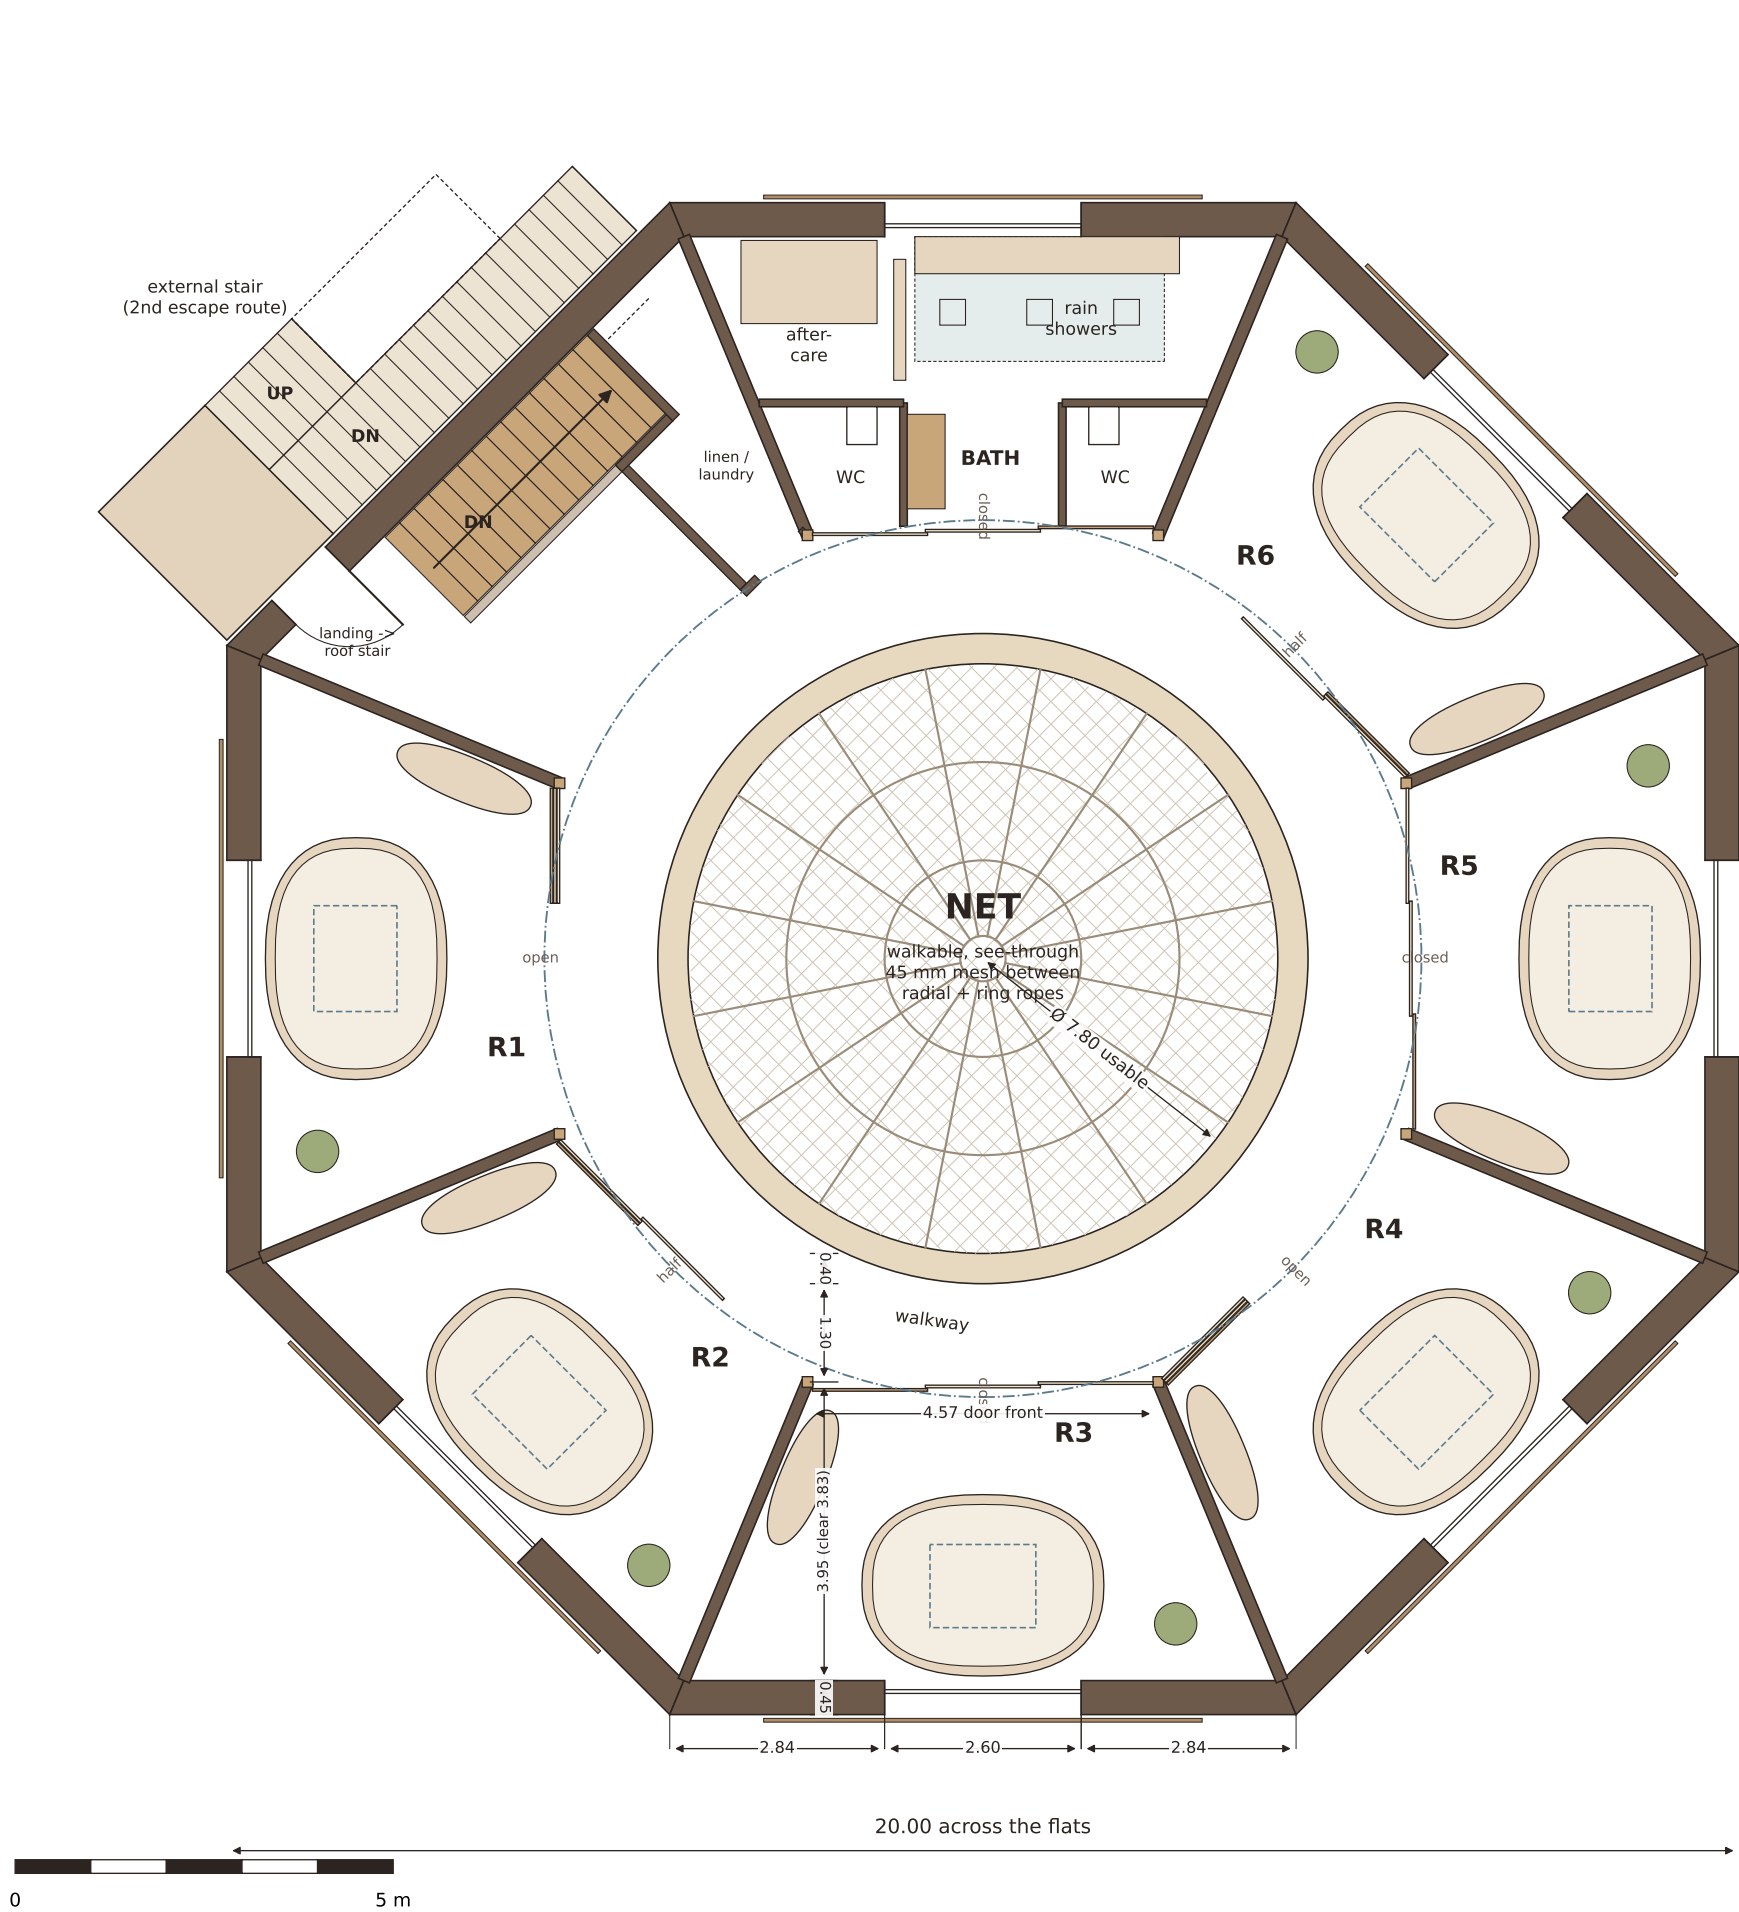

- Rooms (6 × ≈ 23 m², for 1-3 people, also overnight)
- Front: 3 shoji-type panels (oak frame, linen / paper infill): closed / half (1.4 m) / open (2.9 m); a small signal lantern by each door: lit = welcome / ask, dark = private
 - Earthen sleeping nest under the window, clay bench, sheepskins, lanterns, plants – no hotel furniture
 - Big window 2.60 × 1.65 m (sill 0.45 m, fixed safety glass up to 0.90 m), sliding larch shutters outside; the opening part is a rescue window (≥ 0.90 × 1.20 m)
 - Skylight 1.40 × 1.10 m over the nest: walk-on frosted glass in the terrace (light, no view in)
 - Acoustic partitions 160 mm, clay plaster

- Stairs
- Inside: one flight along the NW wall, open to the hall, 22 × 188 mm, going 270 mm, 1.50 m wide; floating oak treads, rope-net balustrade, seating terraces at the bottom, a long clay bench under the flight
 - Outside (NW face): ground -> upper floor -> roof terrace; 2nd escape route and the only way up to the terrace