


Section A-A

North-south through the centre
(looking east)

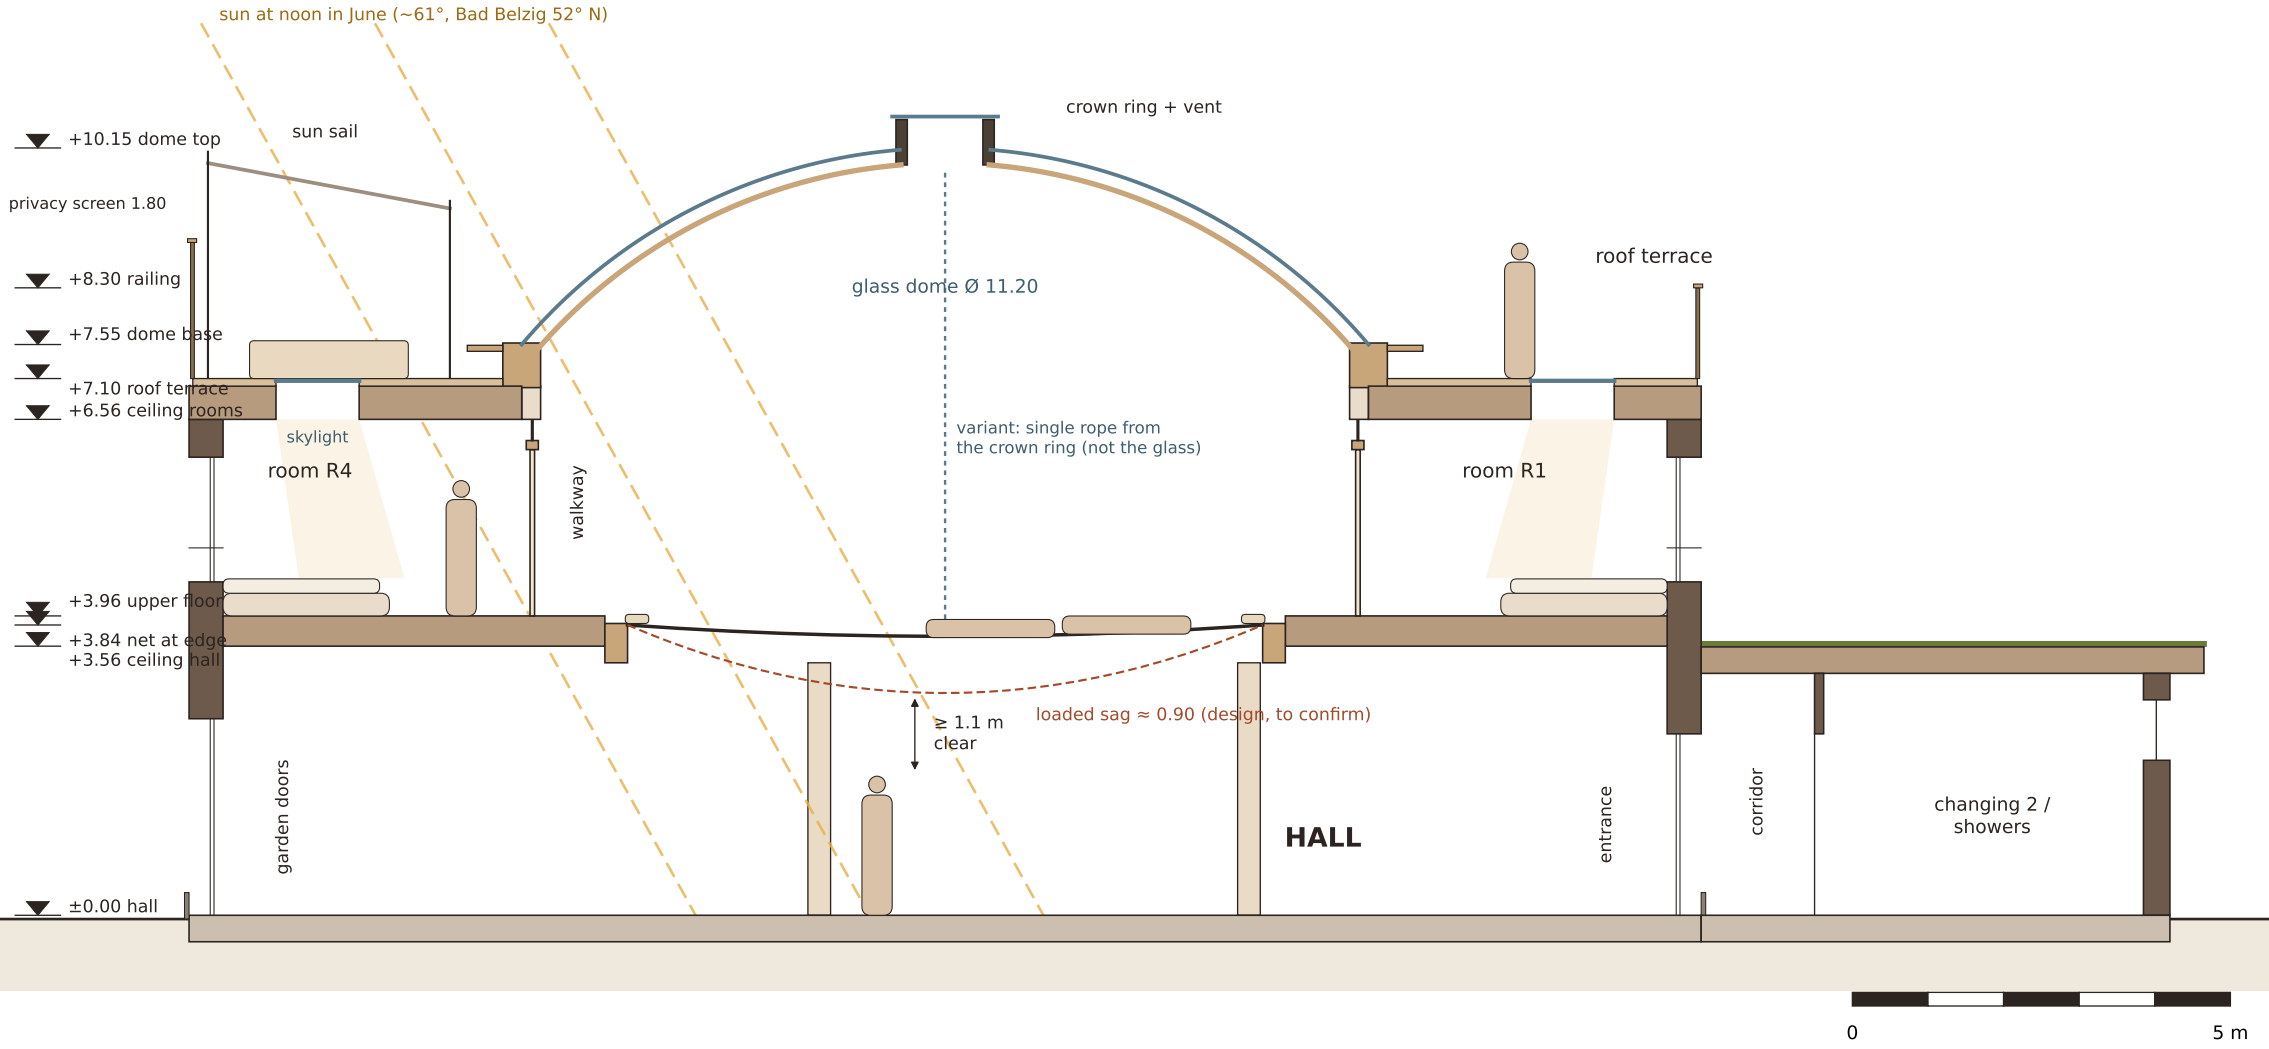

- Net and structure (concept, to be verified)
- Closed steel box ring beam ($\approx 500 \times 300$, timber-clad) on 4 columns takes the inward pull of the net
 - 4 columns: steel tube Ø 219 in a timber casing Ø 30 cm, ≈ 400 kN each (6 columns would allow a lighter ring)
 - 16 radial + 3 ring ropes, fine 45 mm mesh, tensioners at every radial under the pad
 - Net at +3.84 at the edge, 0.15 m pre-sag; design sag ≈ 0.9 m leaves ≥ 1.1 m above a 1.9 m person
 - Variant: one rope from a steel spider in the crown ring (dome structure, not glass)