


Ground floor

Open hall $\approx 290\text{ m}^2$, octagon 20.00 m across the flats
Clear height 3.74 m (3.52 m under the beams)
Only 4 slim columns (steel core $\varnothing 219$ in a $\varnothing 30\text{ cm}$ timber casing) carry the ring beam around the net
Big windows with deep window seats, garden doors to the south, tea / party bar on the NE wall
Small annex on the north face: foyer with coats, WC, tech. Showers + 2 WCs upstairs.
Light: paper pendants, indirect uplight ledge above the windows, clay wall shells

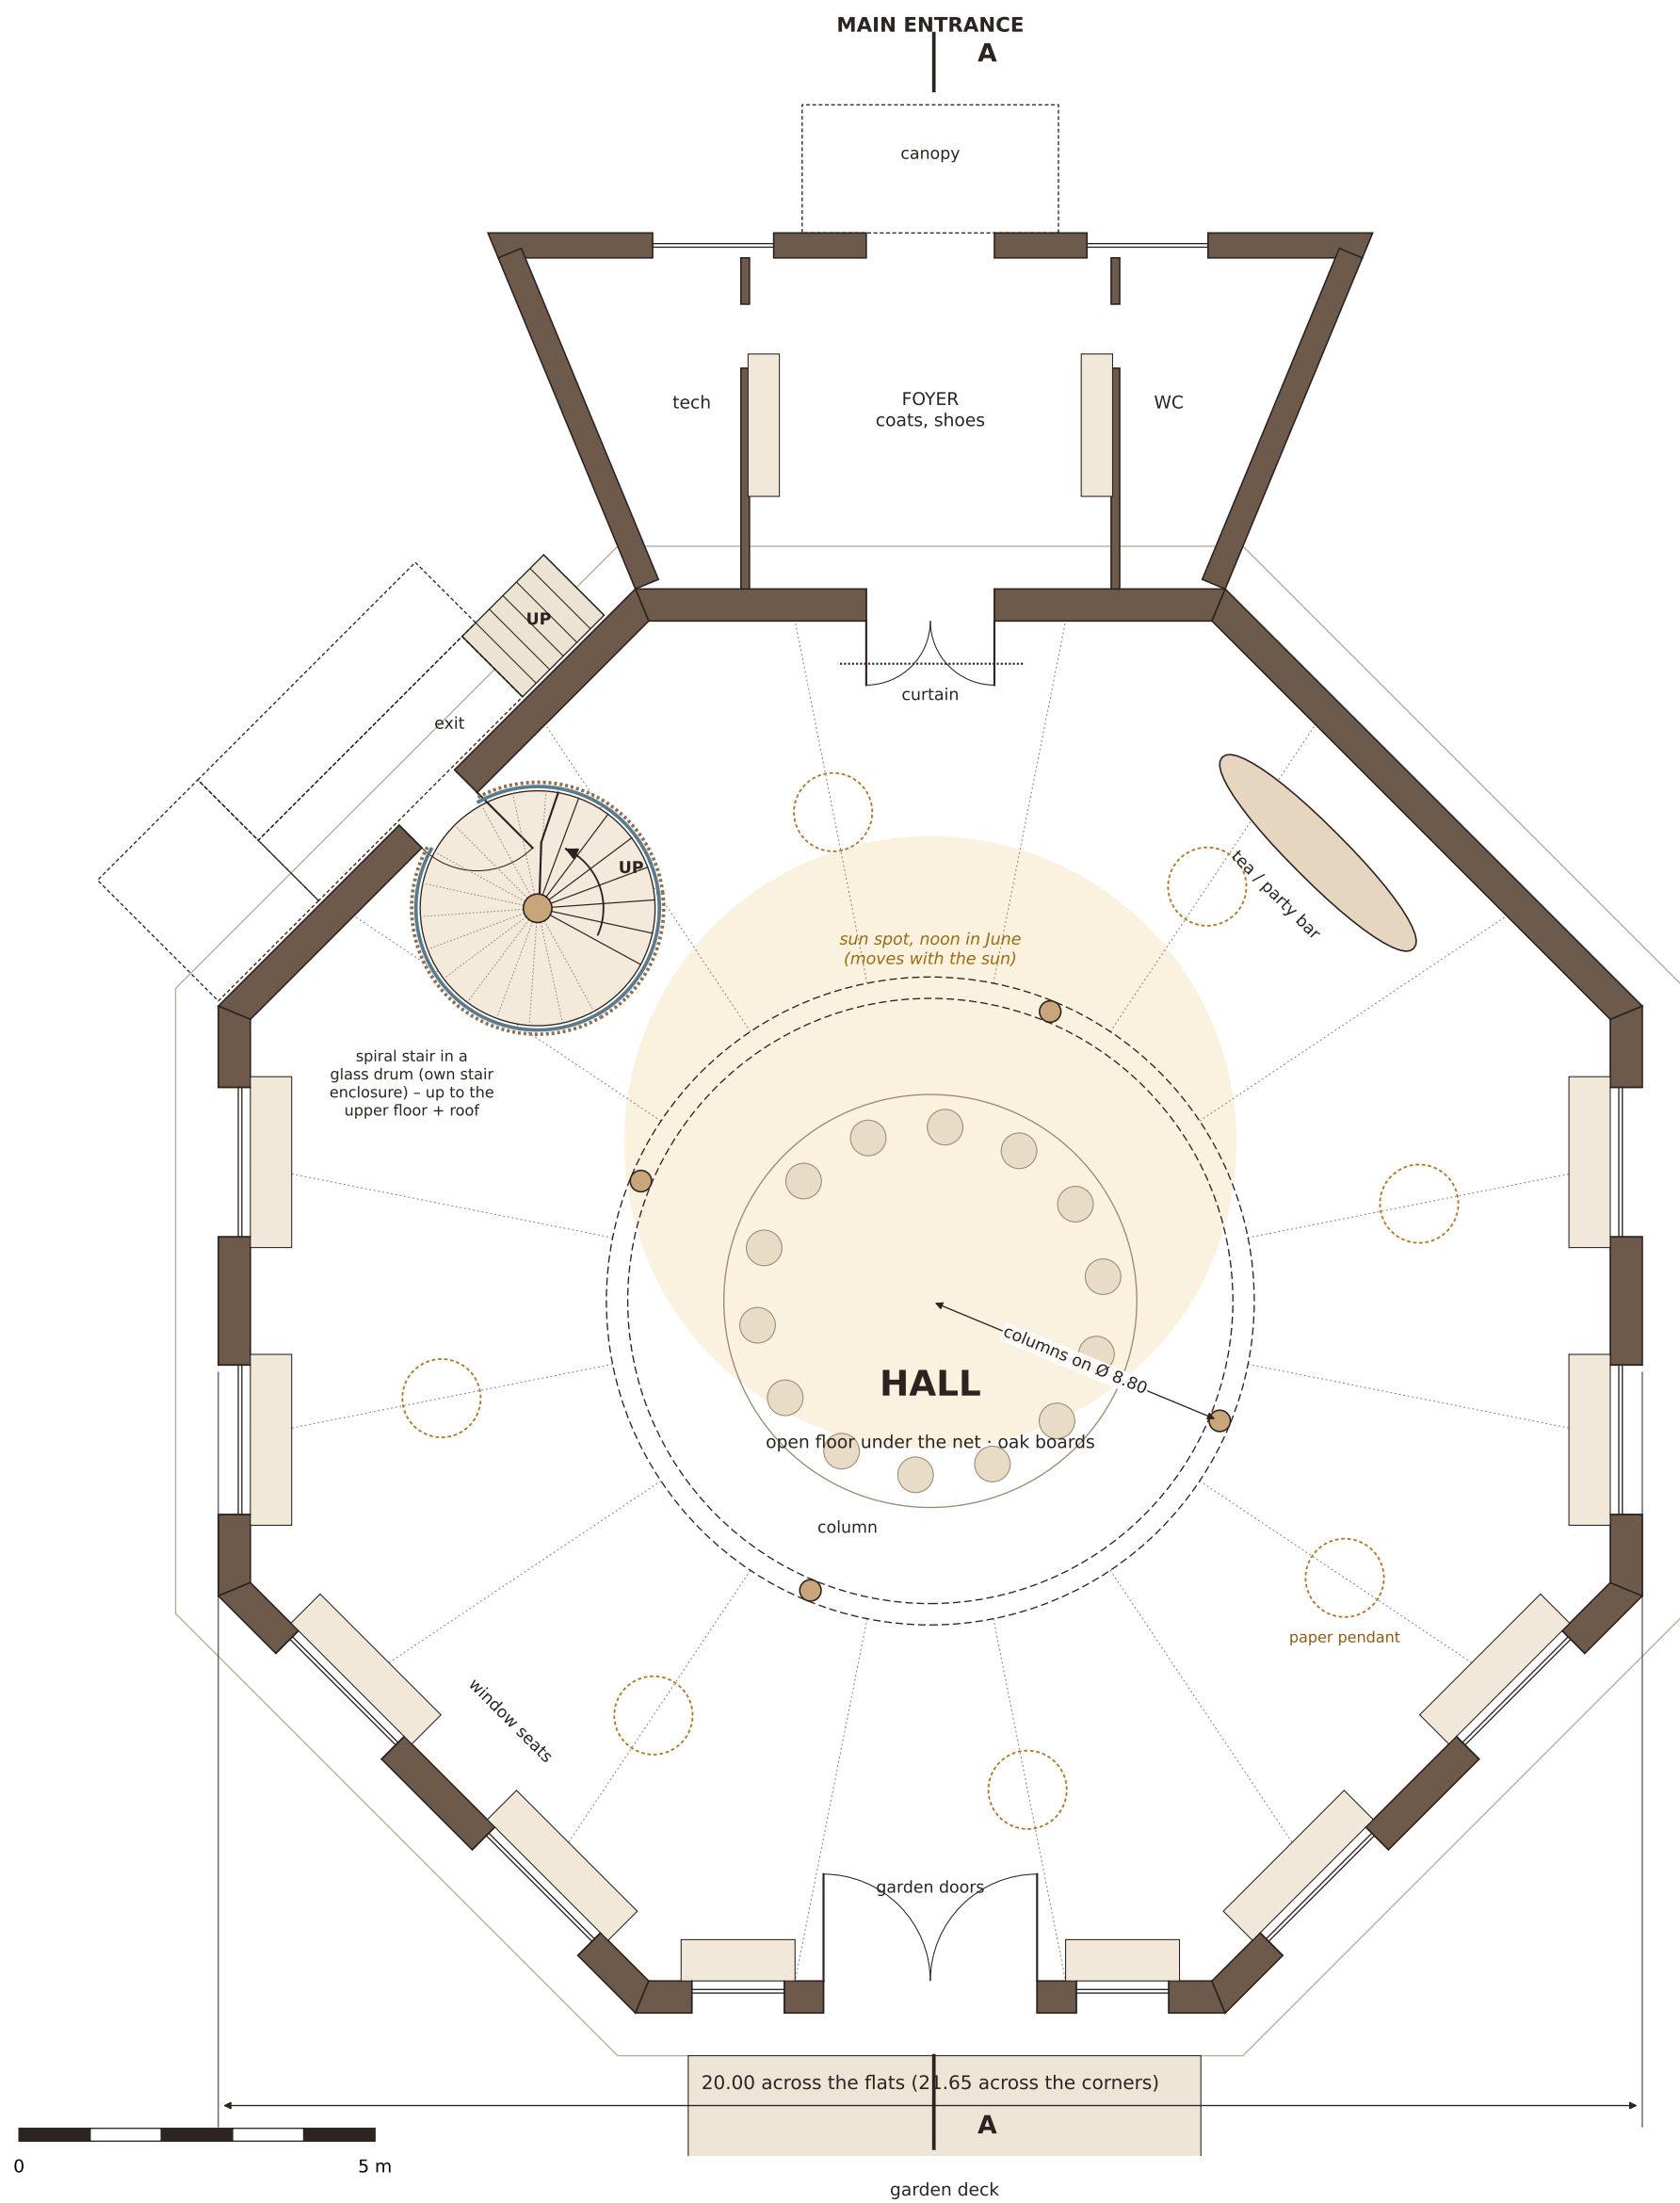

Legend

- cut wall (timber frame, clay inside, larch outside)
- timber column / stair trunk
- fire-rated glass drum around the stair
- above: ring beam, beams, stair, windows
- sun spot through dome + net

Heating & comfort

- Underfloor heating (low-temp., heat pump) in hall and rooms - floors $\sim 26\text{--}28\text{ }^{\circ}\text{C}$, air $\sim 24\text{--}26\text{ }^{\circ}\text{C}$
- Balanced ventilation with heat recovery; vents in the dome crown and stair house for smoke + summer purge
- Clay plaster buffers humidity and sound
- Outside shading on dome and big windows (summer overheating, GEG / DIN 4108-2)