


Upper floor

- From the centre outwards:
- Net Ø 7.80 usable (opening Ø 8.50)
 - Padded edge 0.35 m on the ring beam
 - Ring walkway 1.10 m (up to 1.55 m at the posts)
 - 7 rooms, each $\approx 24\text{ m}^2$: 4.5 m wide at the door, 7.9 m at the straight outer wall, 4.1 m deep
 - Stair segment: spiral stair, WC + shower, door to the external stair
- Clear height in rooms 2.60 m

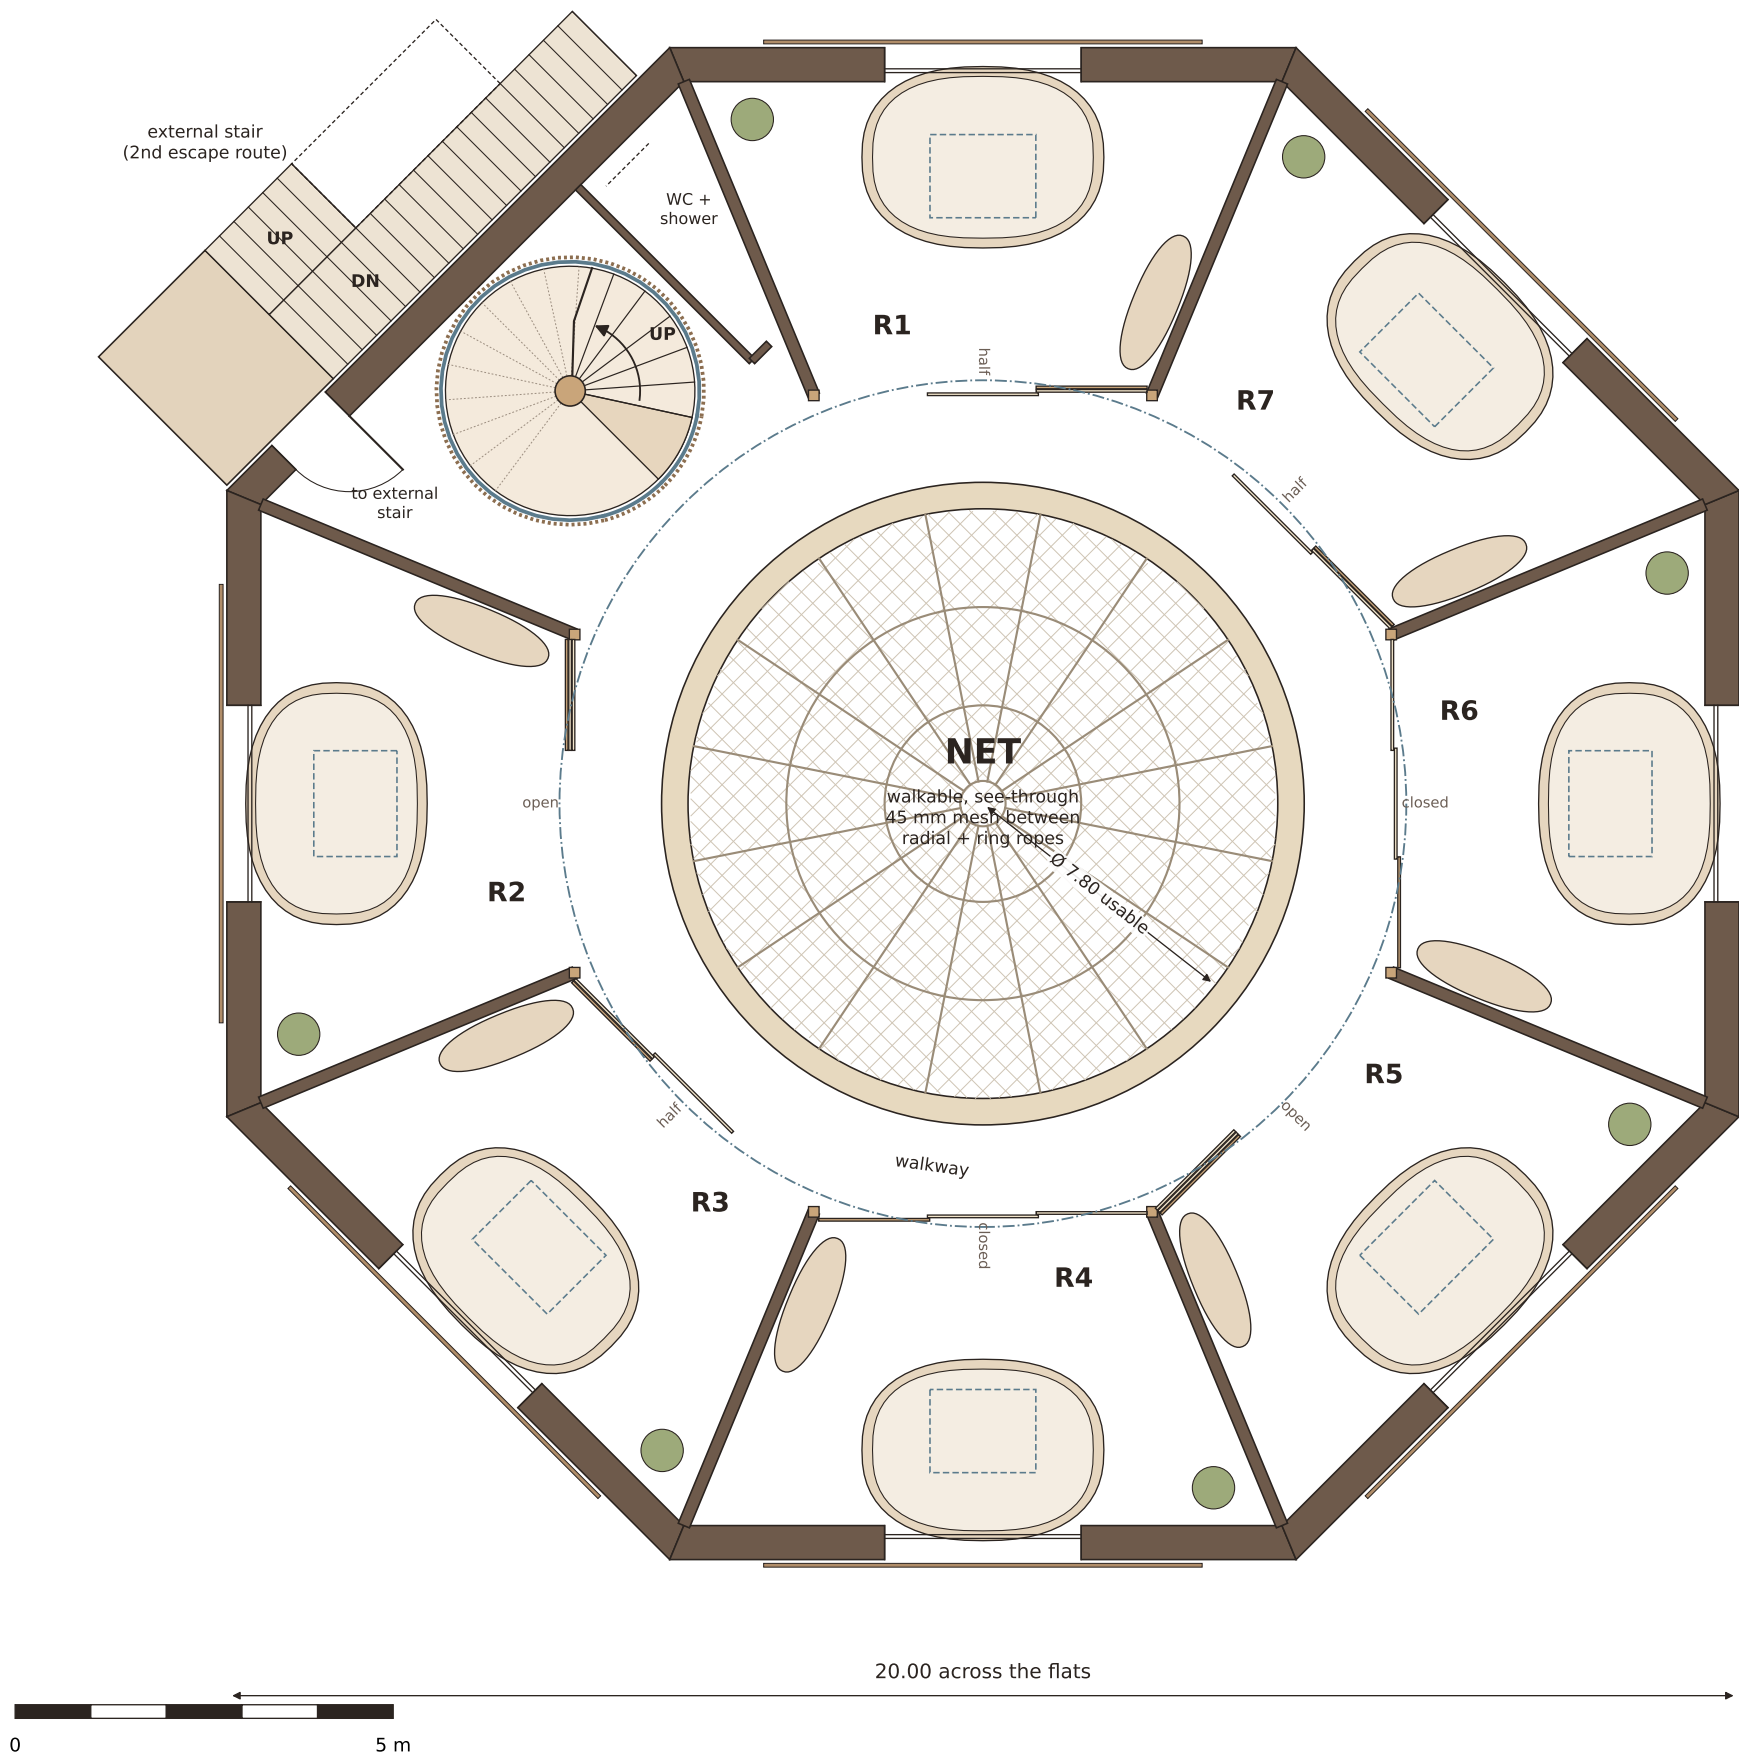

- Rooms ($7 \times \approx 24\text{ m}^2$, for 1-3 people, also overnight)
- Front: 3 shoji-type panels (oak frame, linen / paper infill): closed / half (1.4 m) / open (2.9 m)
 - Earthen sleeping nest under the window, clay bench, sheepskins, lanterns, plants – no hotel furniture
 - Big window $2.60 \times 1.65\text{ m}$ (sill 0.45 m, fixed safety glass up to 0.90 m), sliding larch shutters outside; the opening part is a rescue window ($\geq 0.90 \times 1.20\text{ m}$)
 - Skylight $1.40 \times 1.10\text{ m}$ over the nest: walk-on frosted glass in the terrace (light, no view in)
 - Acoustic partitions 160 mm, clay plaster

- Stair (DIN 18065, as a necessary stair)
- Spiral stair around a timber trunk, Ø 3.3 m, tread width 1.45 m, one turn per storey
 - 22 risers $\times 180\text{ mm}$, going 264 mm on the walking line ($r = 0.925\text{ m}$) · to the terrace $17 \times 185\text{ mm}$
 - Own enclosure: fire-rated glass drum, doors held open on magnets, exit straight outside, smoke vent on top
 - External stair on the same face = 2nd escape route