


# Section A-A

North-south through the centre  
(looking east)

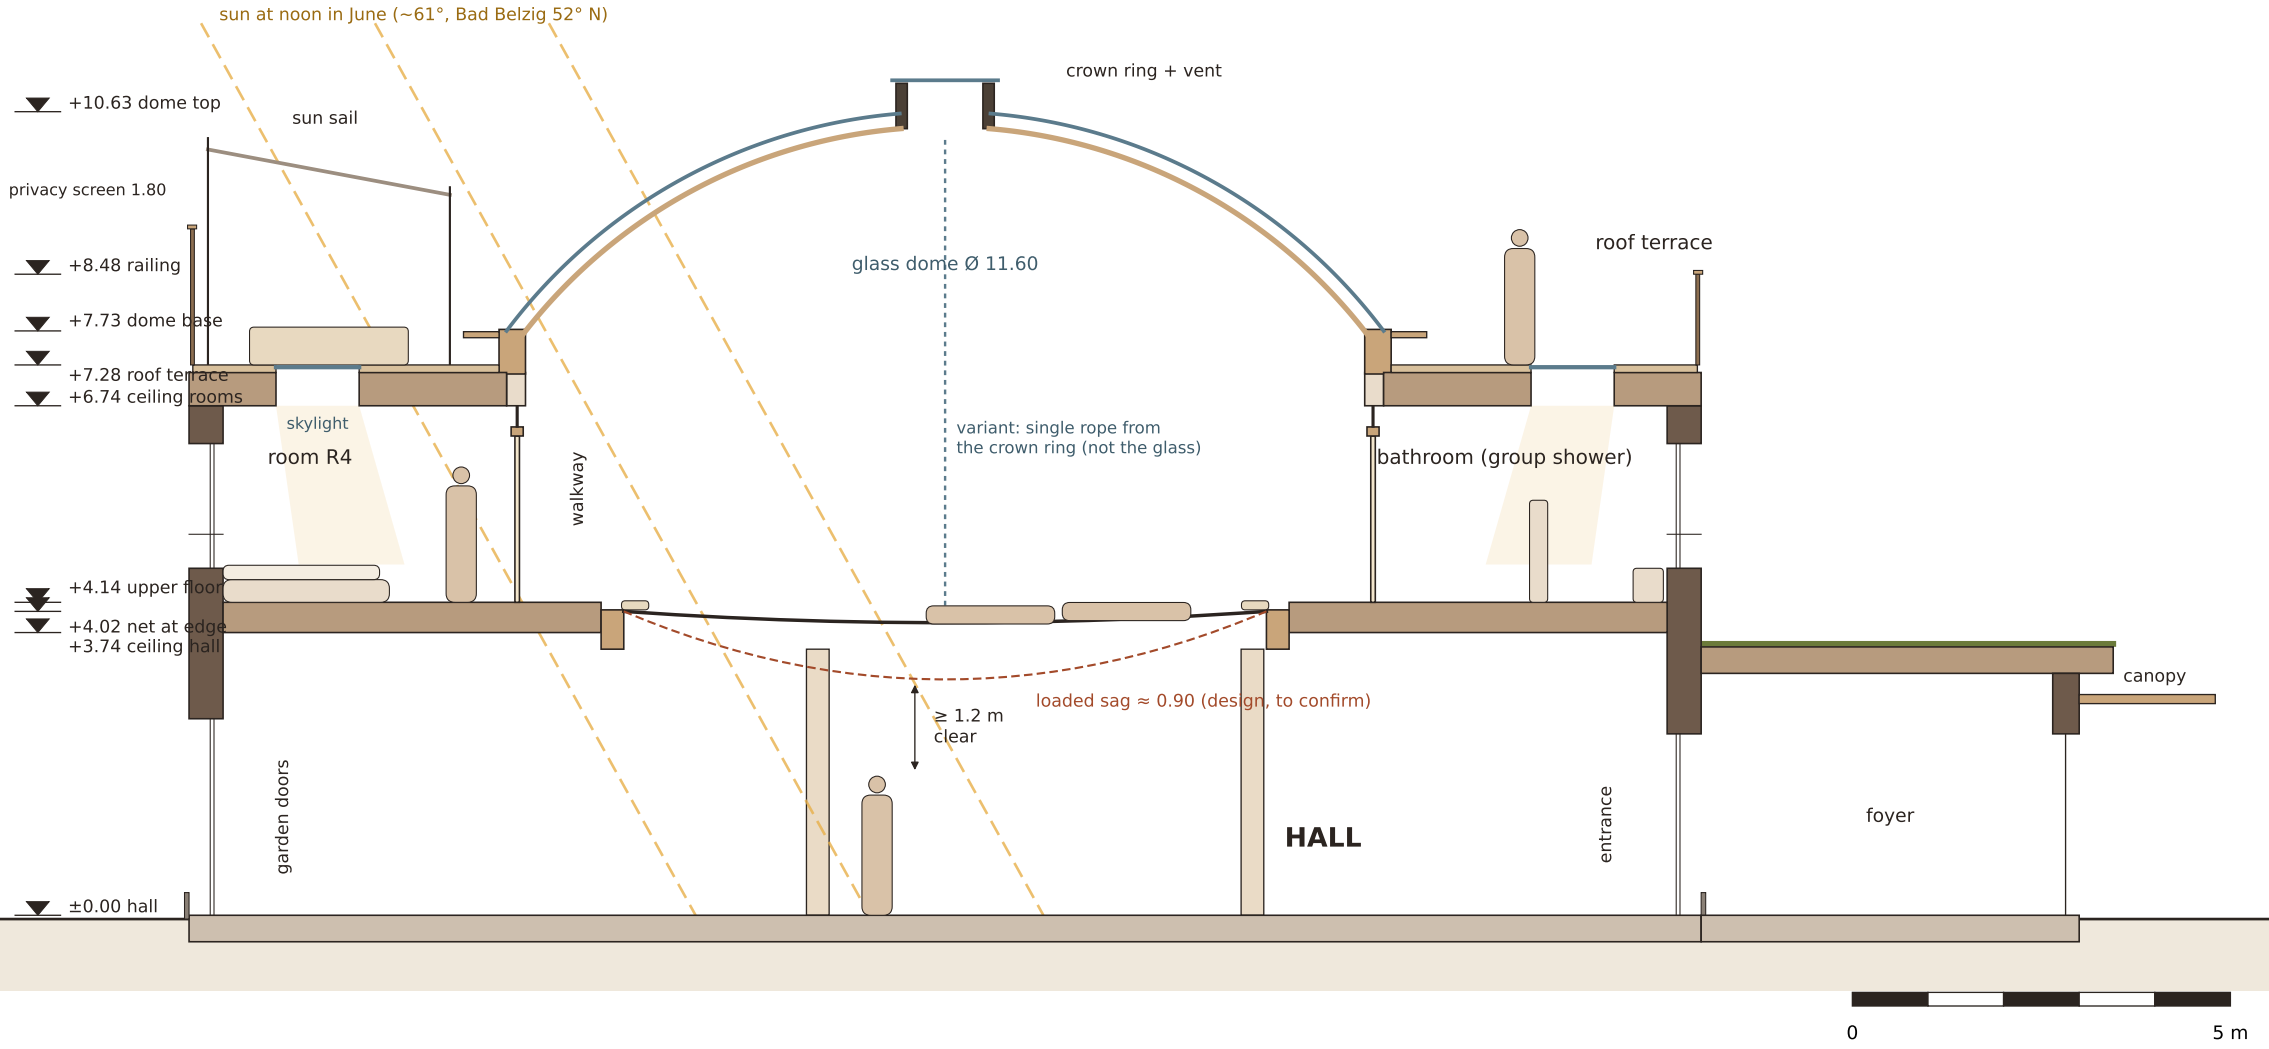

- Net and structure (concept, to be verified)
- Closed steel box ring beam (≈ 500 × 300, timber-clad) on 4 columns takes the inward pull of the net
  - 4 columns: steel tube Ø 219 in a timber casing Ø 30 cm, ≈ 400 kN each (6 columns would allow a lighter ring)
  - 16 radial + 3 ring ropes, fine 45 mm mesh, tensioners at every radial under the pad
  - Net at +4.02 at the edge, 0.15 m pre-sag; design sag ≈ 0.9 m leaves ≥ 1.2 m above a 1.9 m person
  - Variant: one rope from a steel spider in the crown ring (dome structure, not glass)