


Upper floor

- From the centre outwards:
- Net Ø 7.80 usable (opening Ø 8.50)
 - Padded edge 0.35 m on the ring beam
 - Ring walkway 1.10 m (up to 1.38 m at the posts)
 - 9 rooms, each $\approx 17\text{ m}^2$, 3.4 m wide at the door, 5.9 m at the outer wall, 4.1 m deep
 - Half-turn stair in the 10th slot
- Clear height in rooms 2.60 m

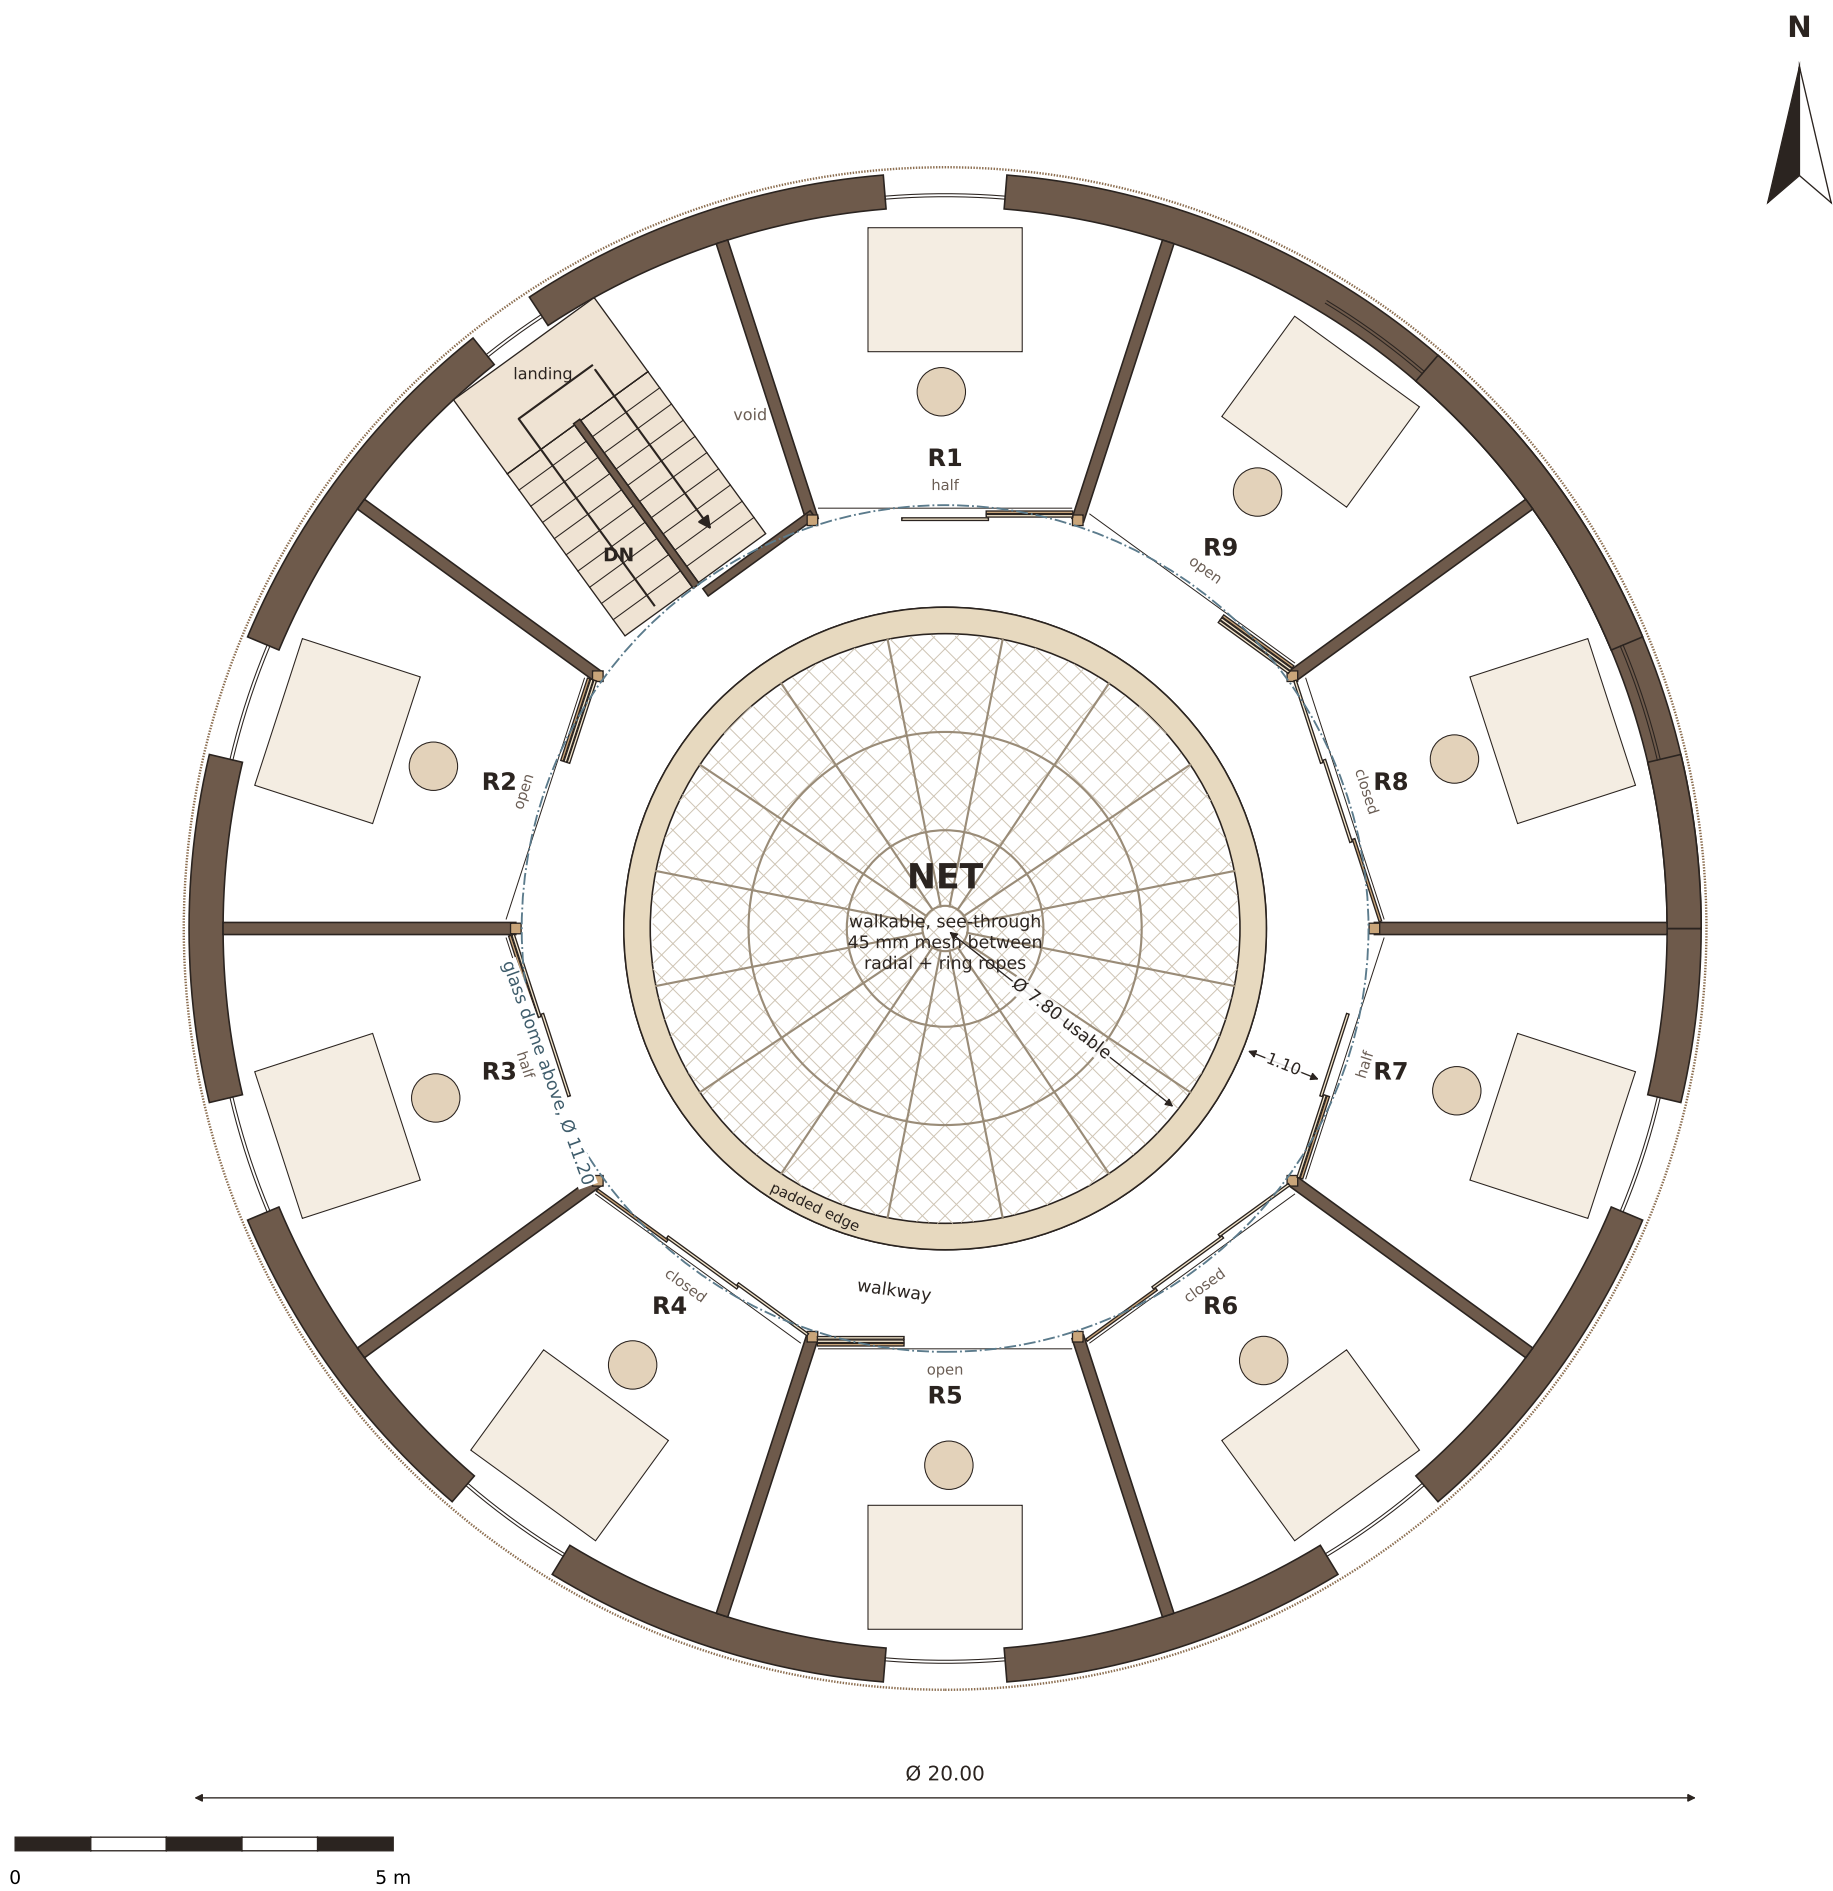

- Rooms
- Front: 3 shoji-type panels (oak frame, linen or paper-laminate infill). One fixed, two sliding: closed / half (1.1 m) / open (2.2 m)
 - One low window per room (sill 0.45 m, 1.6 m wide) behind outside larch battens: light and air, no view in; inside shutter or curtain
 - Acoustic partitions 160 mm, clay plaster
 - Floor mattress, cushions, lanterns, shelf niche

- Stair check (floor to floor 3.96 m)
- 22 risers $\times$ 180 mm, going 265 mm (2R+G = 625)
 - 2 flights $\times$ 11 risers, 1.10 m wide, U-turn
 - Landing 1.15 m deep at the outer wall
 - Needs 3.85 m radial depth - fits the 4.1 m slot. A straight flight (5.6 m going) would not fit.