


# Section A-A

North-south through the centre  
(looking east)

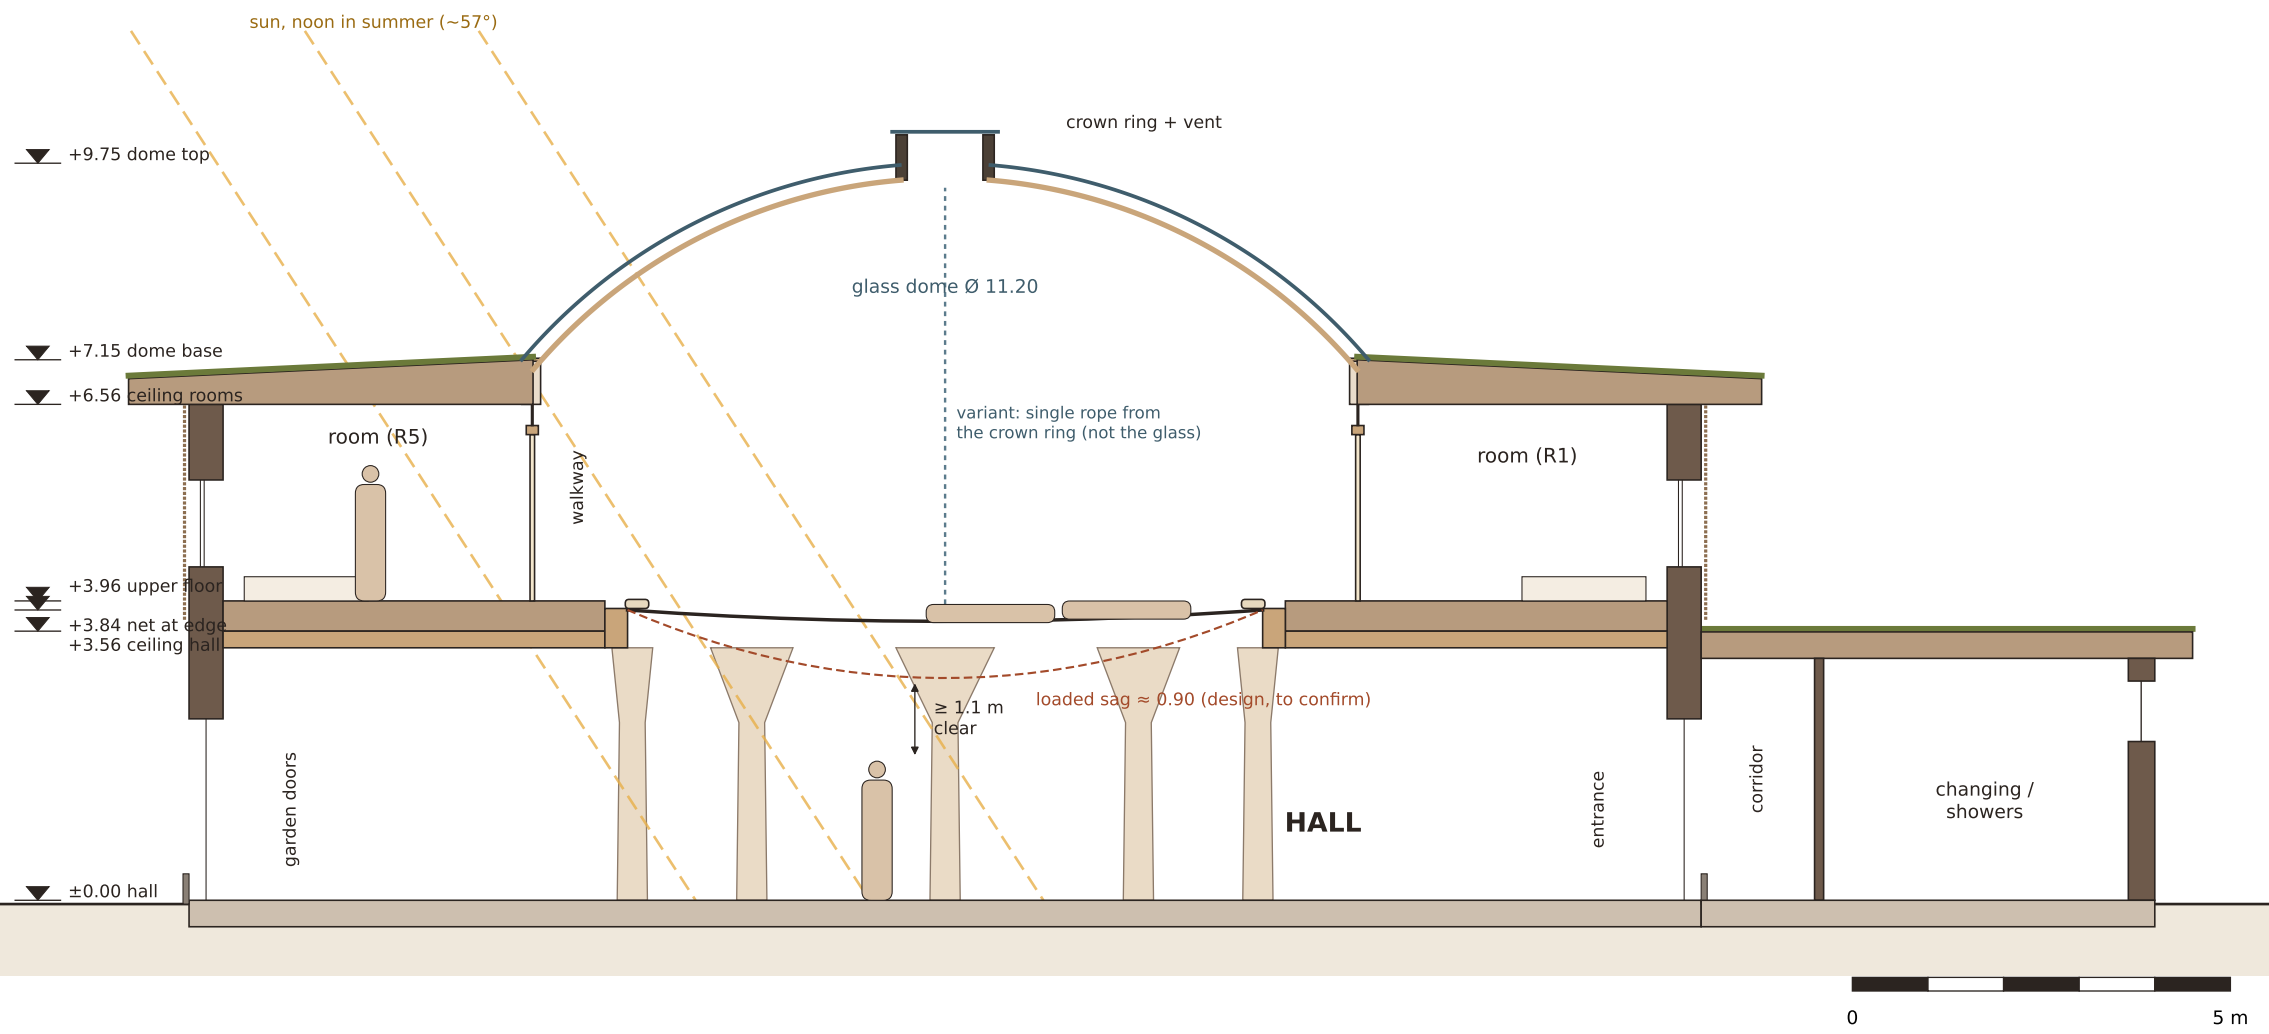

- Net and structure (concept, to be verified)
- Closed ring beam (glulam or steel box) on 10 tree pillars takes the inward pull of the net
  - 16 radial + 3 ring ropes, fine 45 mm mesh, tensioners at every radial under the pad
  - No central support: middle, light and view clear
  - Net at +3.84 at the edge, 0.15 m pre-sag; design sag under load ≈ 0.9 m leaves ≥ 1.1 m above a 1.9 m person below
  - Variant: one rope from a steel spider in the crown ring (dome structure, not glass) - ribs + ring must then carry that load