


Roof terrace

Flat roof over the rooms as a sun terrace
around the dome, deck at +7.10

- South side (SW-S-SE): 6 daybeds, sun sails,
1.80 m slatted privacy screen
- West / east: loungers; north: planters, grasses
- Dome on a 45 cm upstand = bench ring
- Frosted walk-on skylights over each room
- Round stair house (doors both sides) and the
external stair both reach the terrace

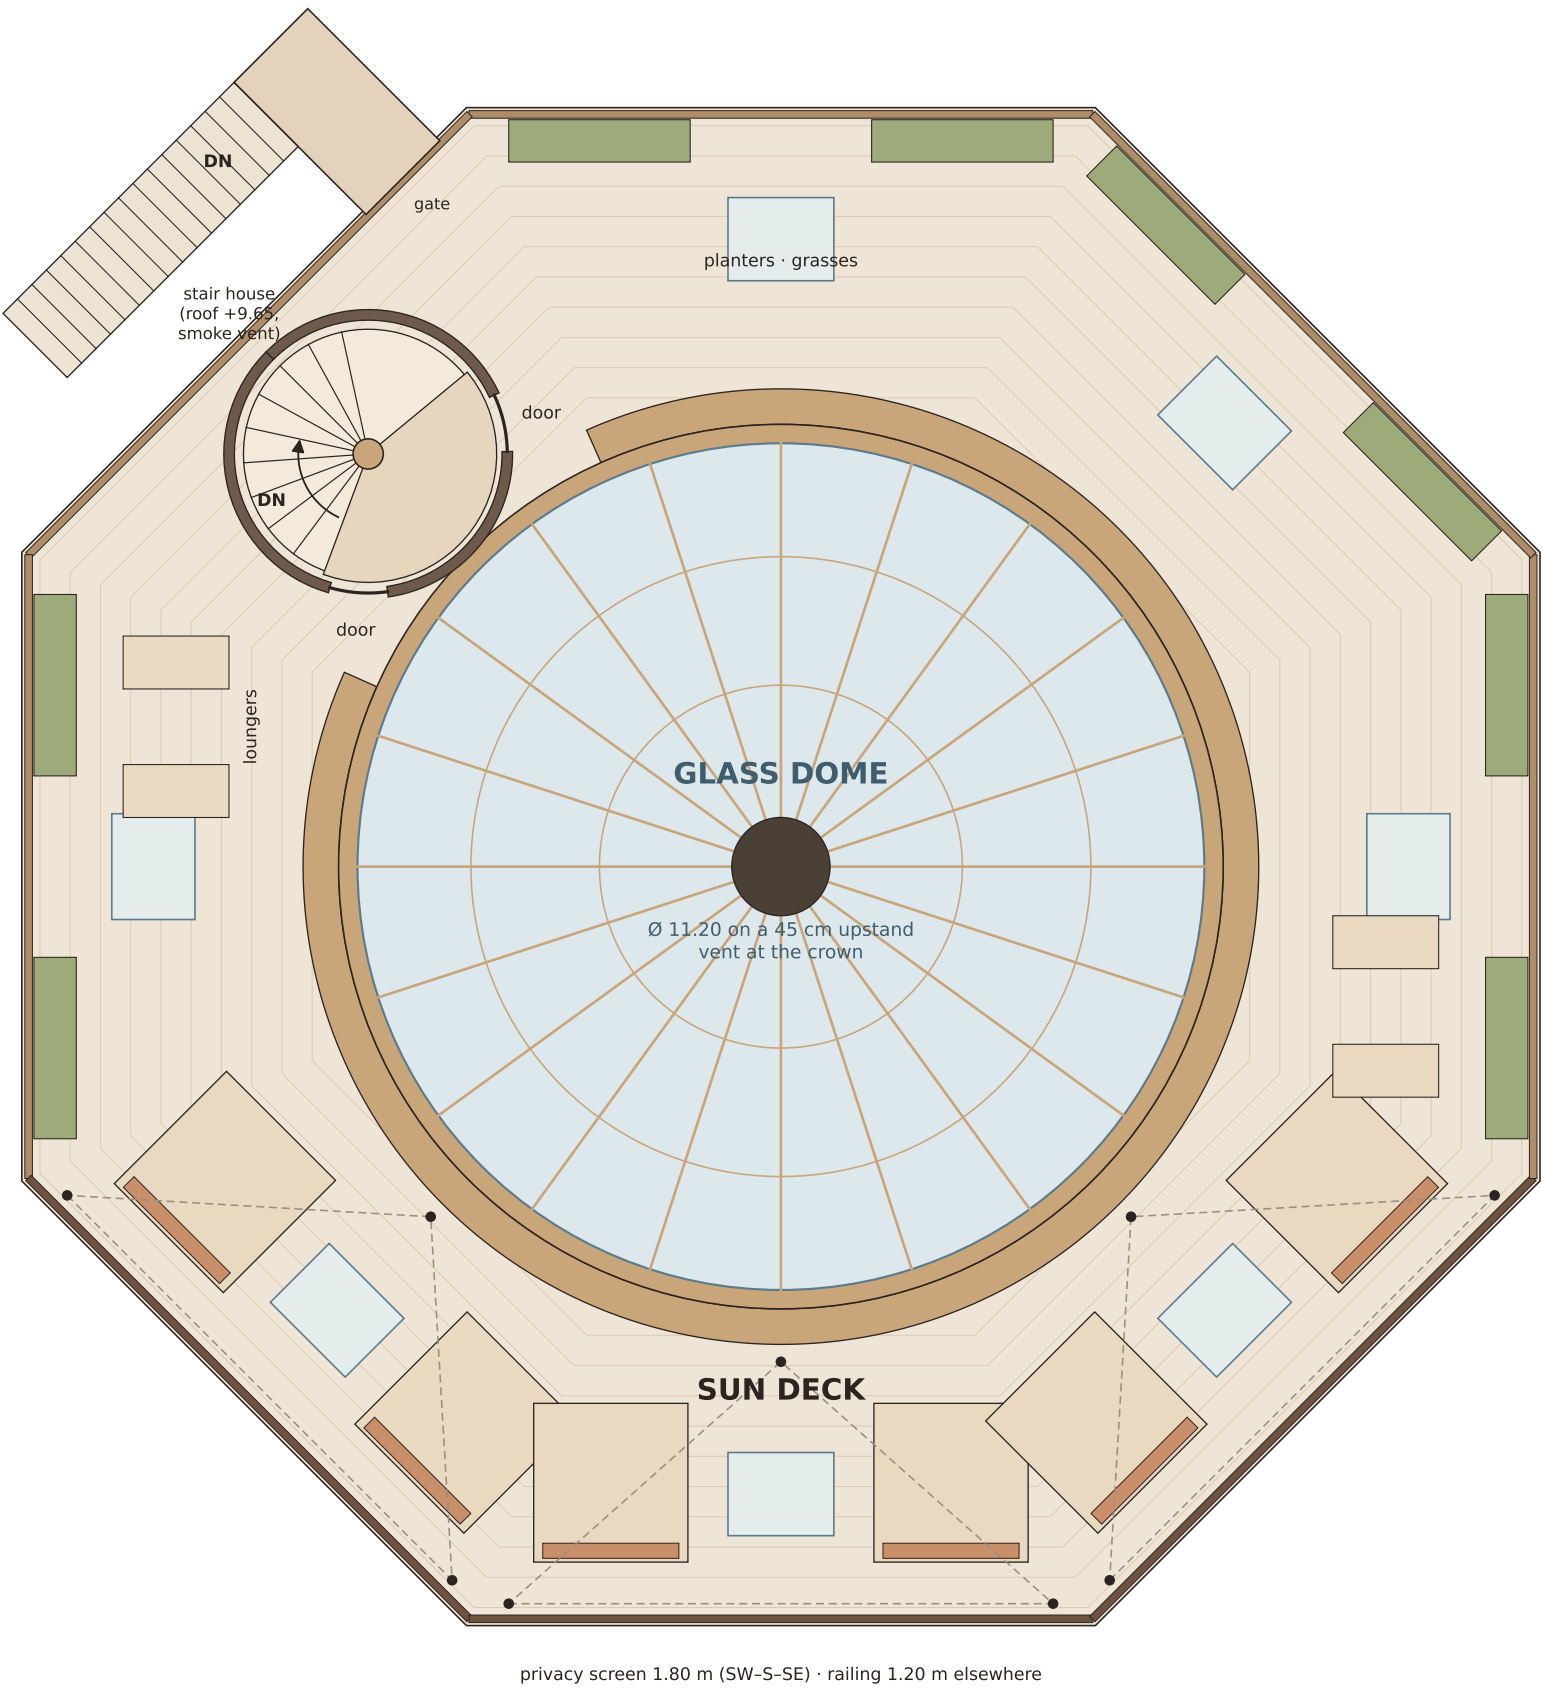

Notes

- Walkable flat roof: imposed load $\approx 4 \text{ kN/m}^2$, falls to internal outlets, deck on pedestals
- Skylights: walk-on laminated safety glass, frosted
- Sun sails are demountable (winter, storms)
- Annex keeps a green sedum roof (not walkable)